


Jiná ověření:

Paré:

Orientační schéma:

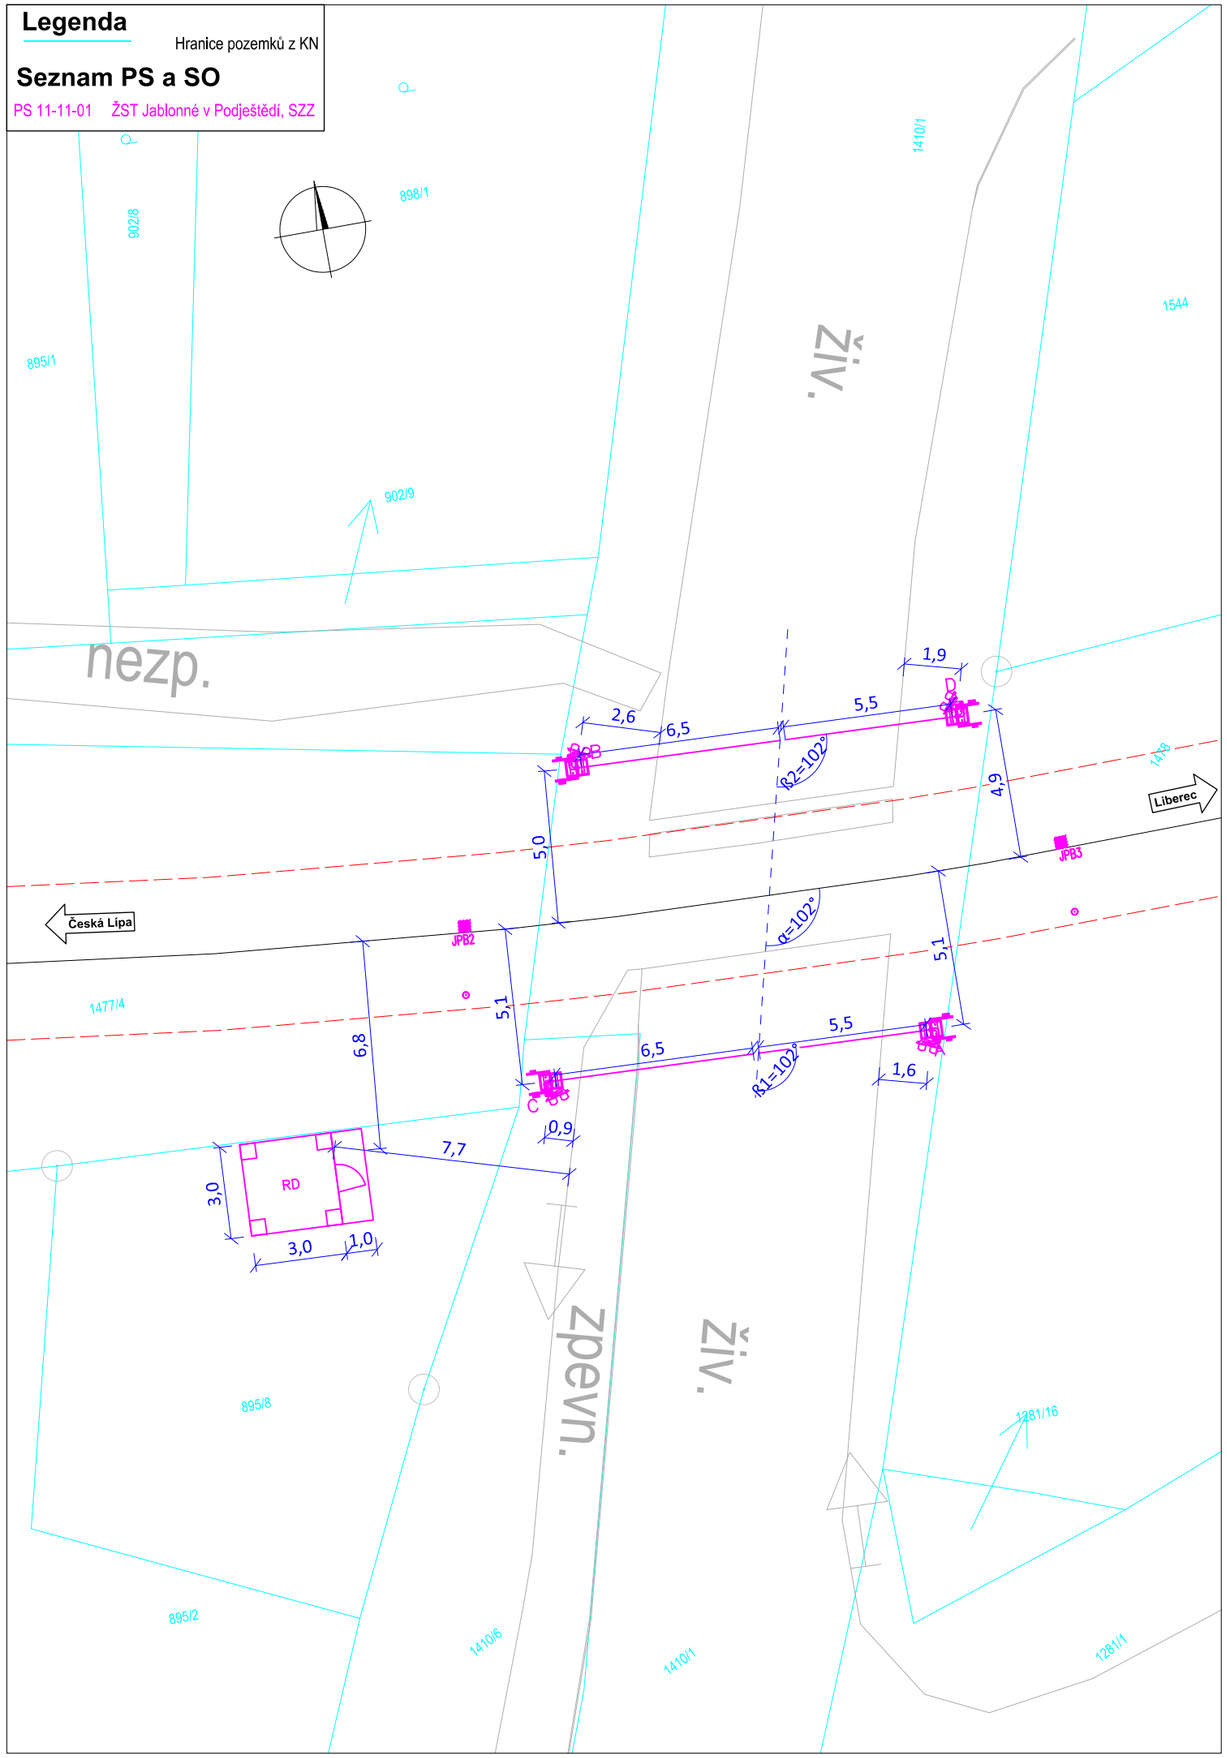

Razítko oprávněné osoby:



Podpis: Datum:

Revize:	Datum:	Popis:	Kontroloval:
000	08.04.2024	Návrh technického řešení DSP k připomínkovému řízení	Ing. Pavol Lipták

Stavebník/Investor:	**Správa železnic, státní organizace**
Adresa:	**Dlážděná 1003/7, 110 00 Praha 1**
Zástupce investora:	**Stavební správa západ**
Adresa:	**Diamond Point, Ke Štvanici 656/3, 186 00, Praha 8**

SPRÁVA ŽELEZNIC

Zhotovitel díla:	**Společnost „VALBEK-PRODEX"**
Adresa:	**Vedoucí společník: Valbek, spol. s r.o.** V Olšinách 2300/75, 100 00 Praha 10
Kontakt:	T: +420 221 592 050 E: info@valbek.cz
	Společník: Valbek SK, spol. s r.o., o.z. V Olšinách 2300/75, 100 00 Praha 10 T: +420 221 592 050 E: info@valbek.cz
Zhotovitel části/objektu:	**VIAMONT Projekt, s.r.o.**
Adresa:	Českobrodská 628, 190 11 Praha 9 – Běchovice
Kontakt:	T: +420 602 320 417 E: info@viamontprojekt.cz
Hlavní projektant (HIP):	**Ing. Pavol Lipták**
Specialista:	**Ing. Milouš Janík**

Název stavby/akce:	**Revitalizace Liberec - Česká Lípa (mimo), přejezd P3415**		Označení investora: **S631500722**
			Zakázka: **20PH61021**
Název části:	Přejezdové zabezpečovací zařízení (PZZ)		Označení části: **D.1.1.3**
Název objektu/dílčí části:	**Železniční přejezd v km 115,242 (P3415), PZZ**		Označení objektu/komplexu: **PS 11-11-01**
Název přílohy:	Situace přejezdu P3415		Číslo přílohy (typ/pořadí): **2 .401**
Název dílčí části přílohy:	-		
Odpovědný projektant: Ing. Marek Štětka	Zpracovatel přílohy: David Pajma	Měřítko: 1:200 Formáty: 2 x A4	Stupeň dokumentace: **DSP**
Kraj: Liberecký	Katastrální území: viz. Technická zpráva	TUDU: 1141 12	Smluvní datum zpracování: **08.04.2024**

Označení investora:	Stupeň dokumentace:	Část:	Objekt:	Podobjekt:	Příloha:	Revize:
S 6 3 1 5 0 0 7 2 2	– D S P X	– D 1 1 0 3	– P S 1 1 1 1 0 1	– – –	– 2 – 4 0 1	– 0 0 0

[Prostor pro další informace]