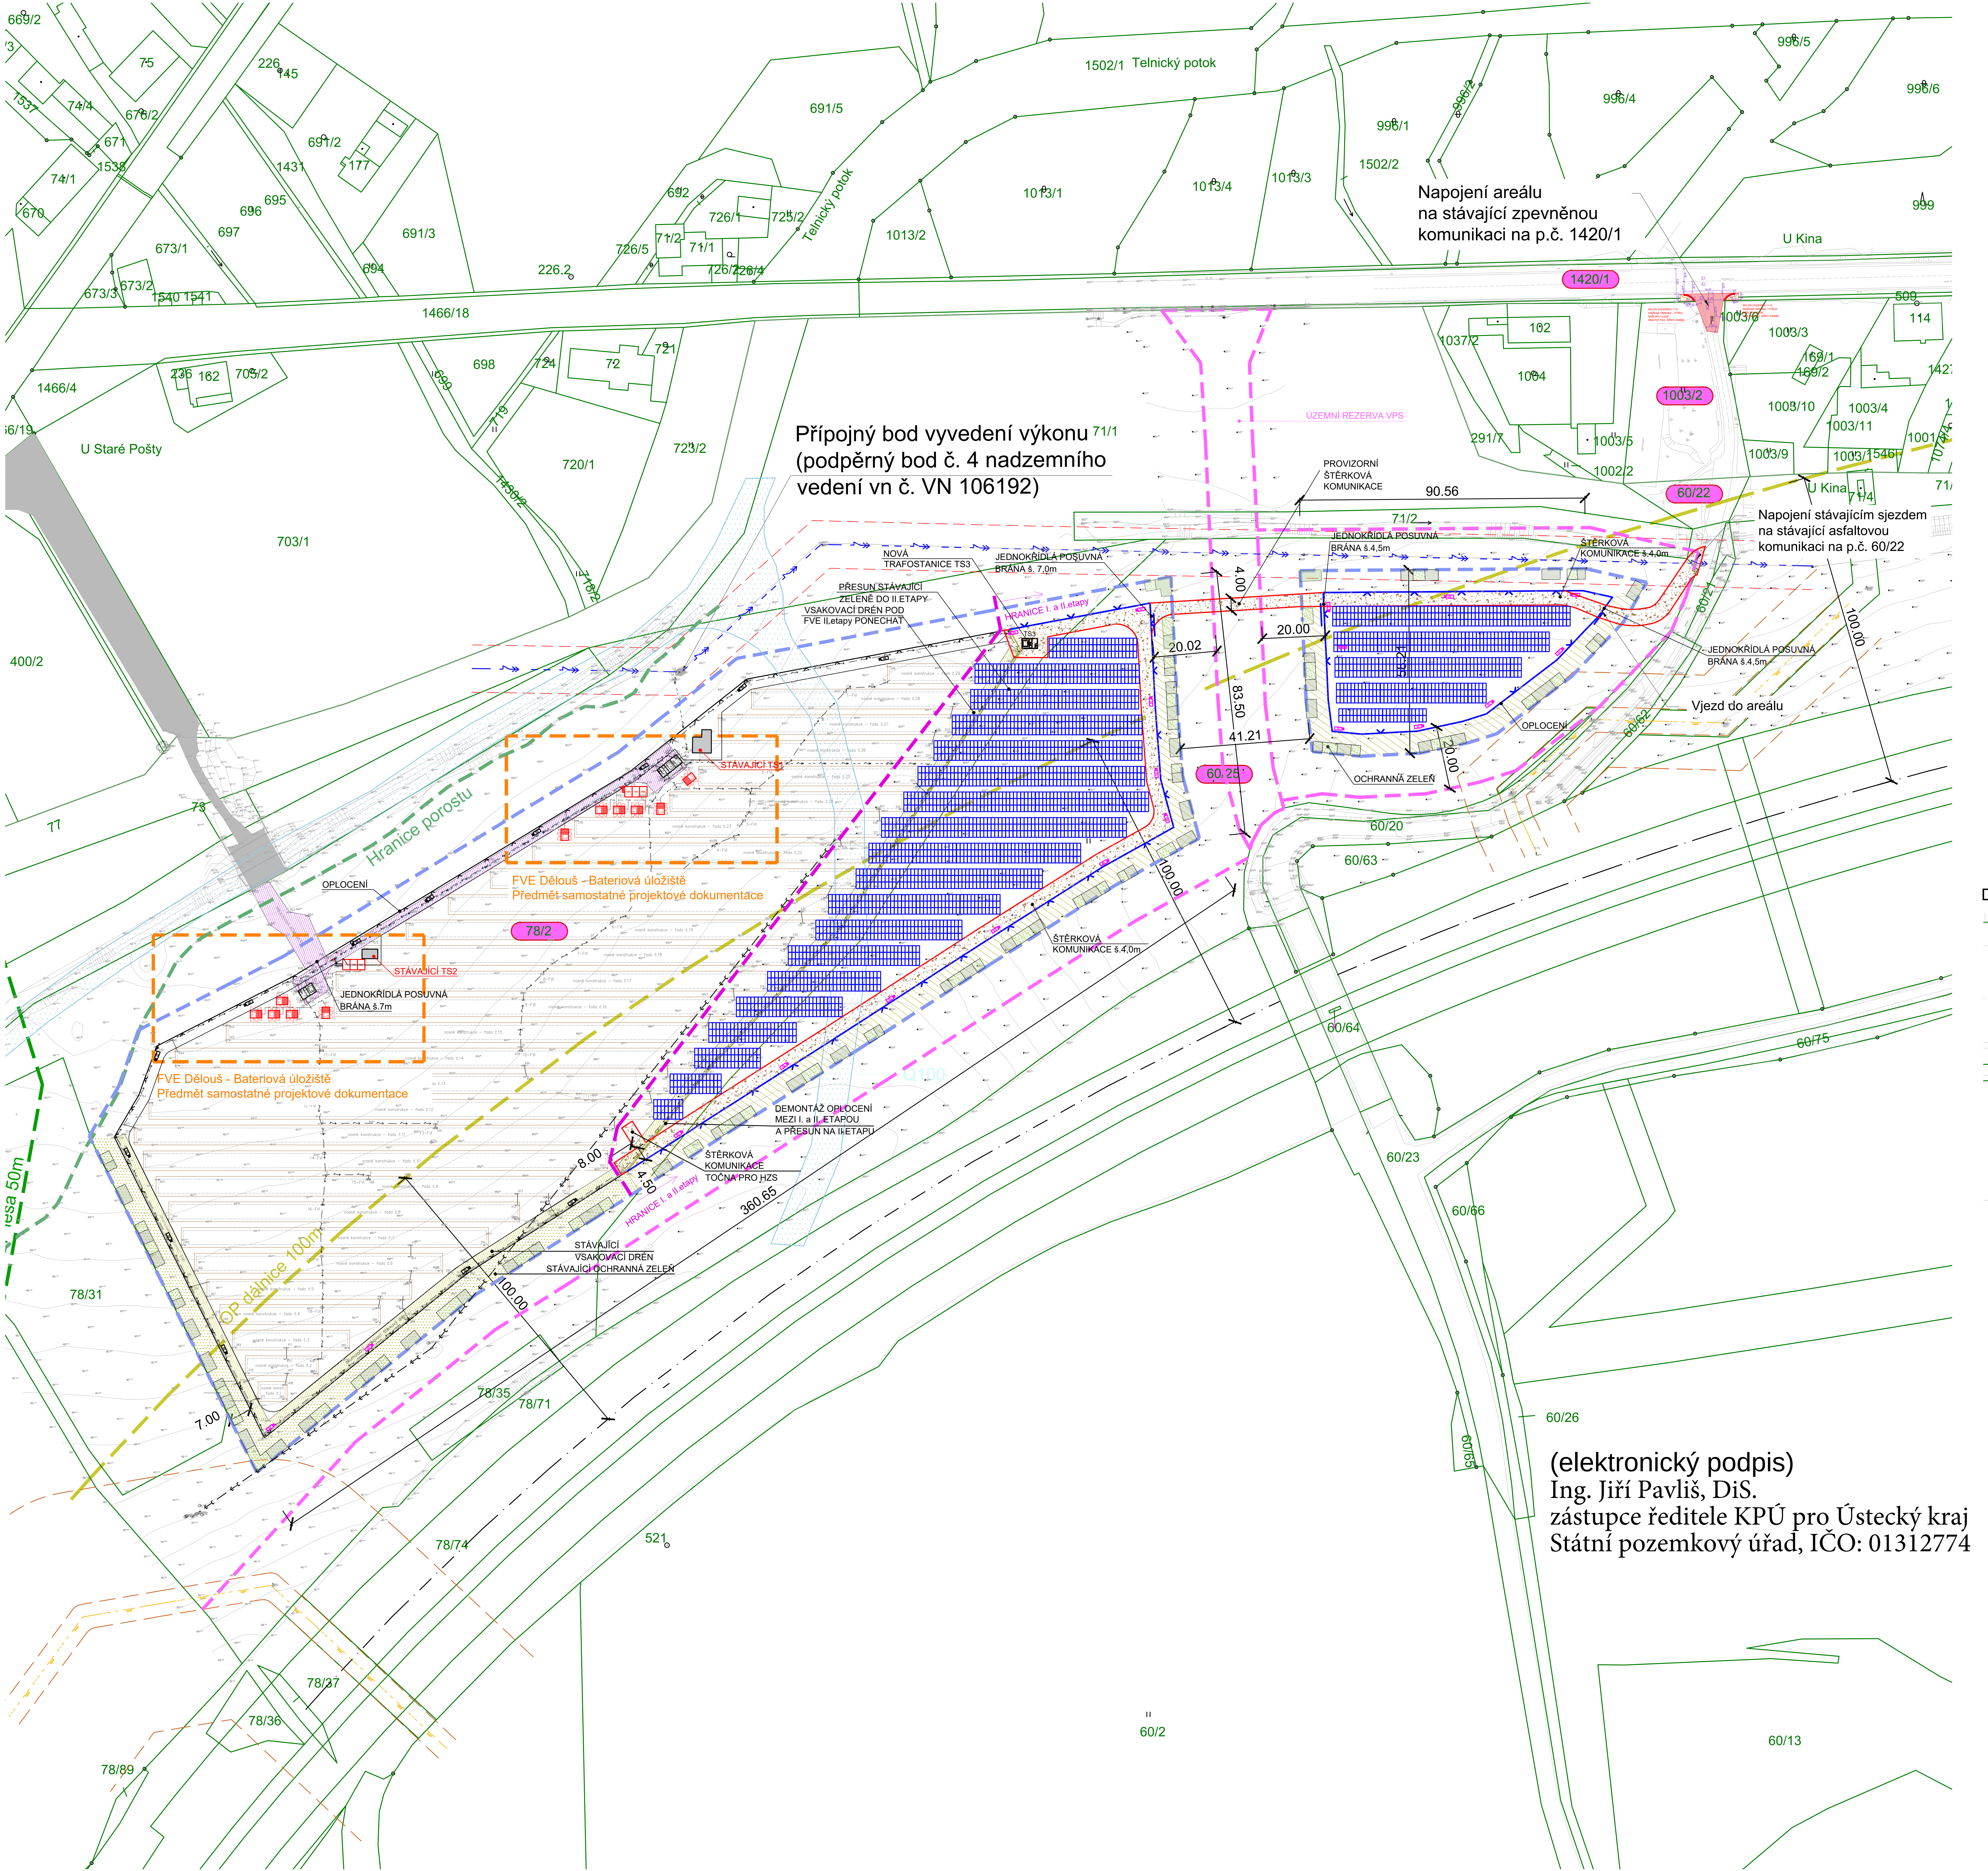

(elektronický podpis)
Ing. Jiří Pavliš, DiS.
zástupce ředitele KPÚ pro Ústecký kraj
Státní pozemkový úřad, IČO: 01312774

LEGENDA

STÁVAJÍCÍ INŽENÝRSKÉ SÍTĚ

- NADZEMNÍ VEDENÍ VN
- OP NADZEMNÍHO VEDENÍ VN
- VTL PLYNOVOD
- OCHRANNÉ A BEZPEČNOSTNÍ PÁSMO VTL PLYNOVODU
- KANALIZACE

STÁVAJÍCÍ INŽENÝRSKÉ AREÁLOVÉ SÍTĚ

- AREÁLOVÉ ROZVODY VN, VYVEDENÍ VÝKONU
- AREÁLOVÉ ROZVODY NN

NOVÉ INŽENÝRSKÉ SÍTĚ

- PODZEMNÍ VEDENÍ VN
- OCHRANNÉ PÁSMO VN
- PODZEMNÍ VEDENÍ NN

POPIS

- ZÁJMOVÉ ÚZEMÍ FVE
- HRANICE ÚZEMNÍHO PLÁNU
- *VYMEZENÍ OCHRANNÉHO PÁSMA 20m K OPLOCENÍ*
- OCHRANNÉ PÁSMO DÁLNICE
- KATASTRÁLNÍ HRANICE POZEMKU
- STÁVAJÍCÍ OPLOCENÍ
- DEMONTOVANÉ OPLOCENÍ
- NOVÉ OPLOCENÍ
- GEODETICKÉ ZAMĚŘENÍ AREÁLU
- STÁVAJÍCÍ FVE I.ETAPY
- NAVRŽENÉ FVE 2.ETAPY
- 78/2 KATASTRÁLNÍ ČÍSLO POZEMKU
- 78/2 POZEMKY DOTČENÉ STAVBOU
- ZPEVNĚNÁ ŠTĚRKOVÁ KOMUNIKACE
- STÁVAJÍCÍ ZPEVNĚNÁ ŠTĚRKOVÁ KOMUNIKACE I.ETAPY
- STÁVAJÍCÍ AKUMULAČNÍ ŠTĚRKOVÝ DRÉN
- STÁVAJÍCÍ OCHRANNÁ ZELEŇ
- ODSTRANĚNÁ A PŘESUNUTÁ OCHRANNÁ ZELEŇ V KOLIZI S II.ETAPOU
- NAVRŽENÁ OCHRANNÁ ZELEŇ
- STÁVAJÍCÍ IP KAMERA
- NOVÁ IP KAMERA

DETAIL ŘEŠENÉHO SJEZDU. BLIŽŠÍ SPECIFIKACE viz SAMOSTATNÁ ČÁST PD

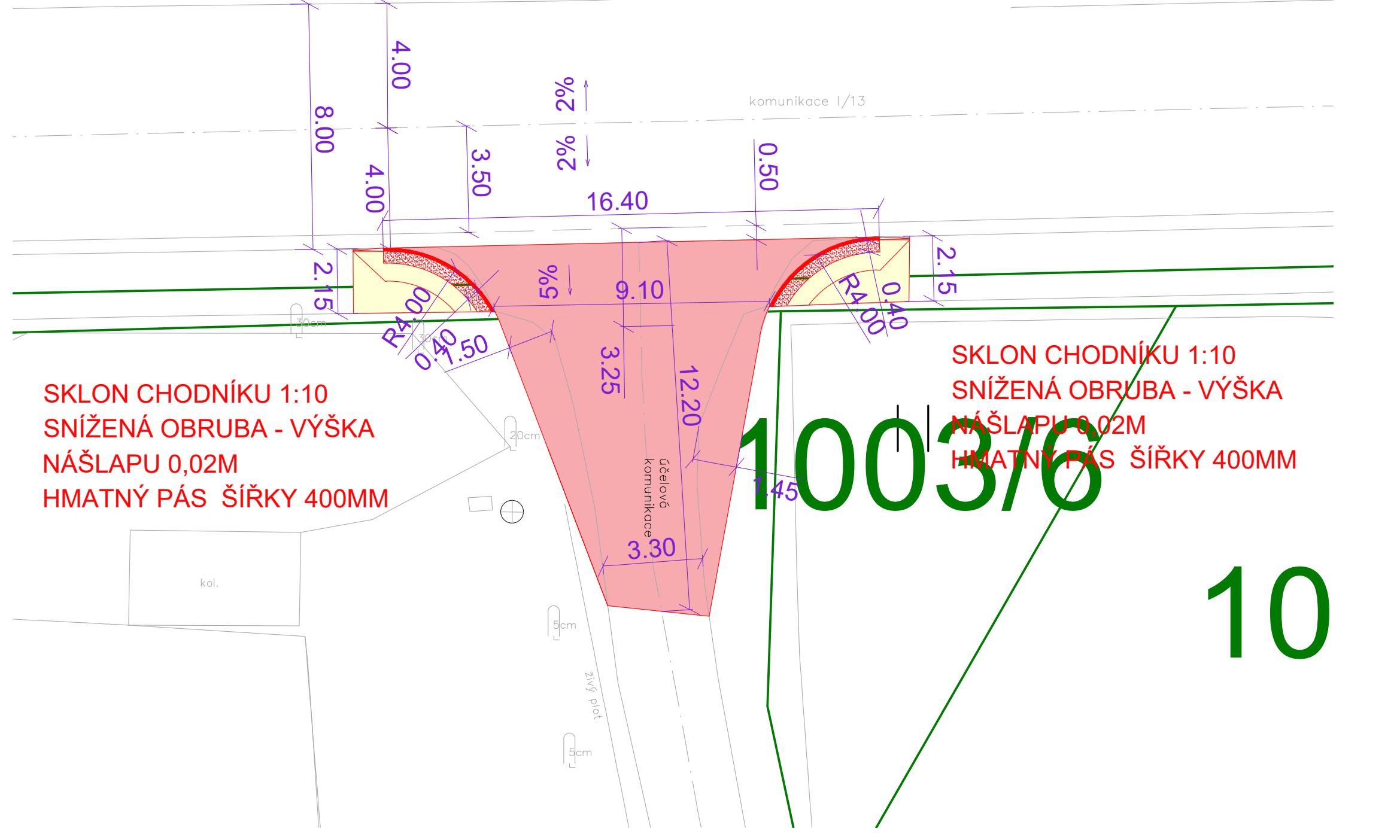

Výškový systém Bpv
Souřadnicový systém S-JTSK

GENERÁLNÍ PROJEKTANT:

Reinka, spol. s r.o.,
adresa: Štefánikovo náměstí 1702/18,
Chomutov 430 01
email: p.bucifal@reinka.cz
tel.: +420 602 468 530

PROJEKT:

FVE Dělouš I. – 2. Etapa

OBCHODNÍ SOUBOR: CPI 020 – KOORDINACE

STAVEBNÍ OBJEKTY: C. SITUACE STAVBY

ČÁST DLE VYHLÁŠKY: C.

NÁZEV VÝKRESU: KOORDINAČNÍ SITUAČNÍ VÝKRES

Reinka, spol. s r.o.
adresa: Štefánikovo náměstí 1702/18,
Chomutov 430 01
email: p.bucifal@reinka.cz
tel.: +420 602 468 530

HIP:	Lukáš Maciejewski	INVESTOR:	CPI Green, a.s.
VYPRACOVAL:	Lukáš Maciejewski	GENERÁLNÍ DODAVATEL:	Czech Property Investments, a.s.
KONTROLOVAL:	Ing. Přemysl Bucifal	GENERÁLNÍ PROJEKTANT:	Reinka spol. s r.o.
MĚŘÍTKO:	1:1000, 1:250	KONCEPT ARCHITEKT:	Czech Property Investments, a.s.

STAVBA, JEDNOTKA:	STUPEŇ:	OBCHODNÍ SOUBOR:	ČÍSLO DOKUMENTU:	REVIZE:	DATUM:
Dělouš_FVE	DPZ	CPI 020	C.3	00	2024-10-07