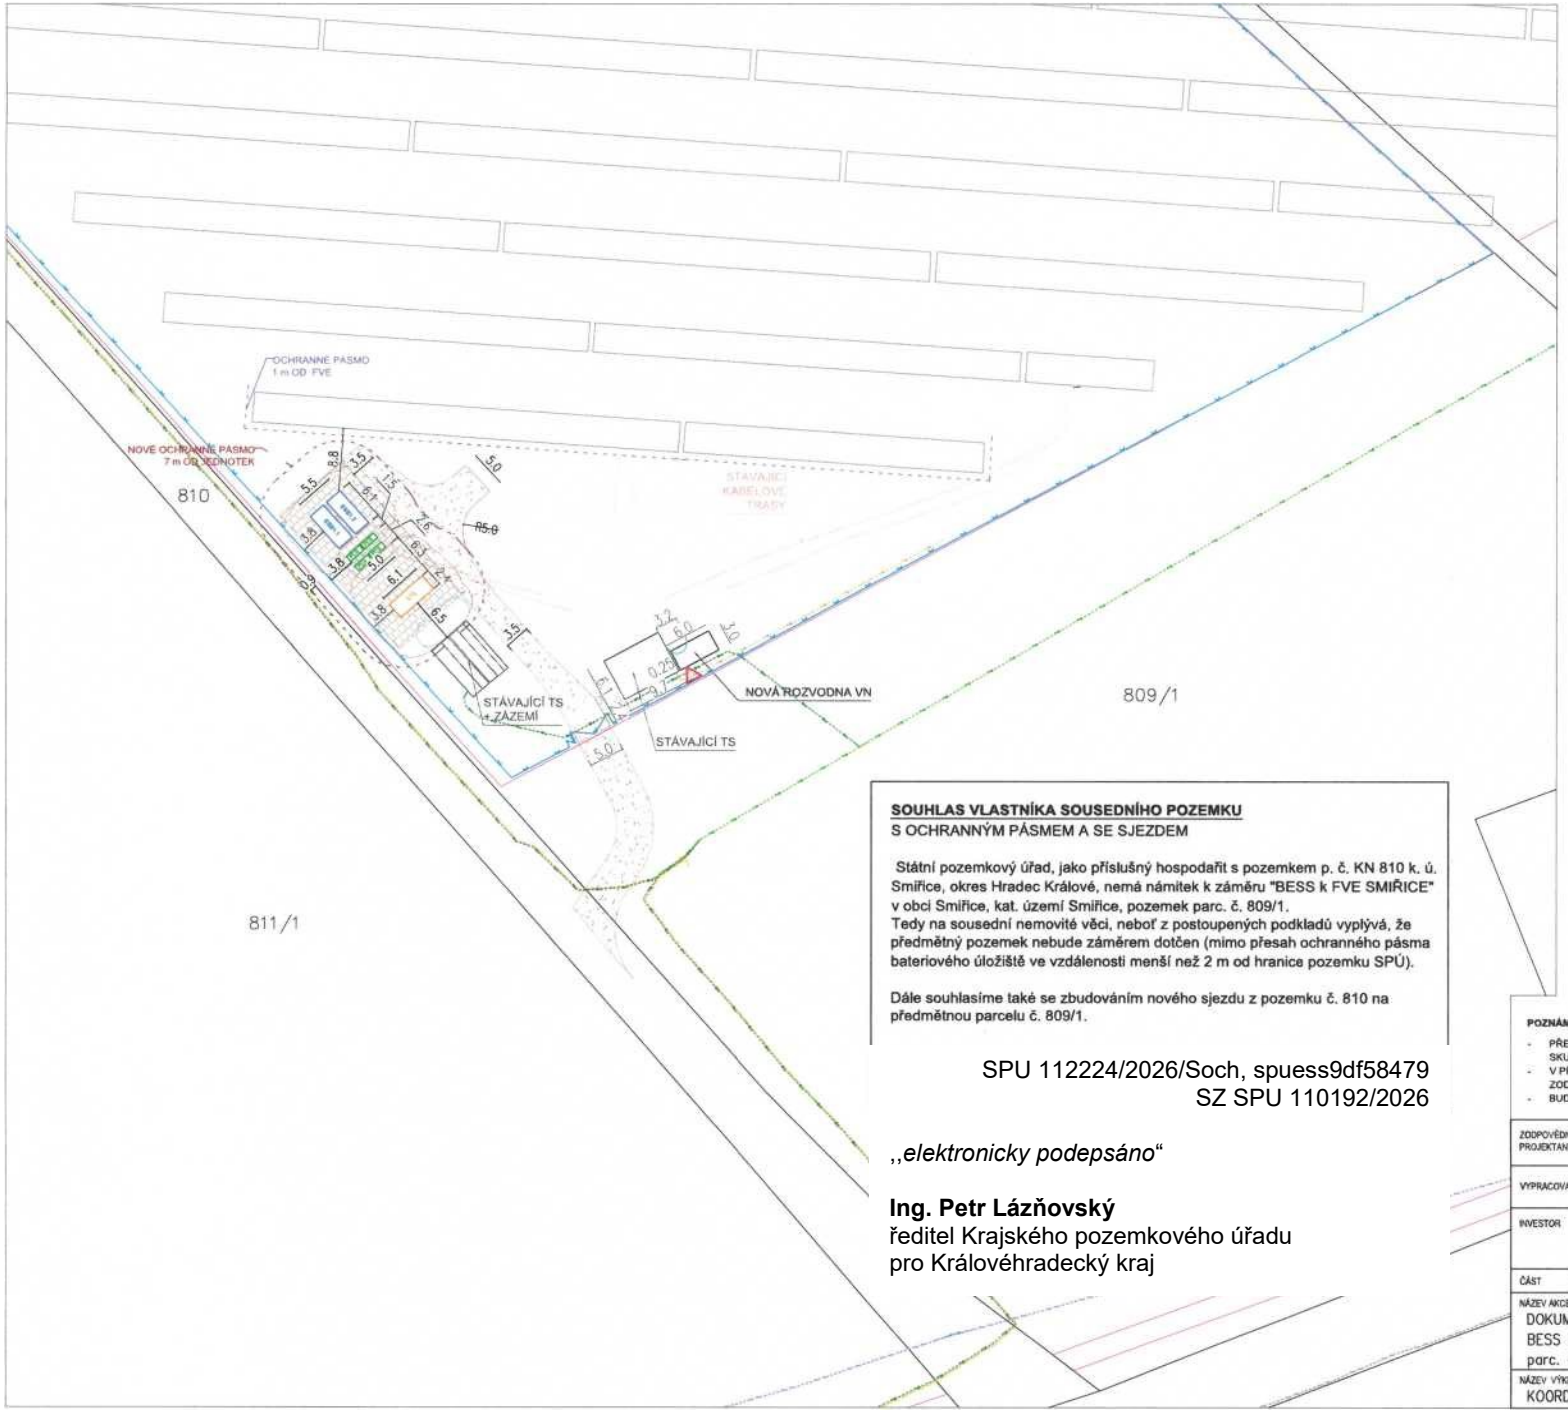


LEGENDA

KATASTRÁLNÍ HRANICE POZEMKU

688/8 OZN. PARCELY

VĚCNÁ BŘEMENA DLE ČÚZK

STÁVAJÍCÍ FVE

STÁVAJÍCÍ OPLOCENÍ

LEGENDA NOVÝCH ČÁSTÍ

ESS POLOHA BATERIOVÉHO KONTEJNERU 2,2 MWh

STS POLOHA TRAFOKONTEJNERU JUPITER-6000K-H1

PCS POLOHA STŘÍDAČŮ

POLOHA NOVÉ ROZVODNY

POŽÁRNĚ NEBEZPEČNÝ PROSTOR JEDNOTEK

dle PBŘ žádné, otvory, žádná okna, na střeše nesmí být hořlavý povrch - asf. pás musí být pod štěrkem

NOVÉ OCHRANNÉ PÁSMO 7 m OD JEDNOTEK

VCHOD DO NOVÉ ROZVODNY

NOVÁ ZPEVNĚNÁ CESTA, PROPUSTNÁ

NOVÉ ZPEVNĚNÉ PLOCHY, PROPUSTNÉ

LEGENDA STÁVAJÍCÍCH SÍTÍ

SDĚLOVACÍ VEDENÍ - METALICKÉ (CETIN)

SOUBĚH PODZ VN DO 35 kV + SDĚLOVACÍ (ČEZ)

NADZEMNÍ VN DO 35 kV (ČEZ)

PODZEMNÍ VEDENÍ VN DO 35 kV (ČEZ)

LEGENDA NAVRHOVANÝCH SÍTÍ

NOVÁ PŘÍPOJKA VN

SOUHLAS VLASTNÍKA SOUSEDNÍHO POZEMKU
S OCHRANNÝM PÁSMEM A SE SJEZDEM

Státní pozemkový úřad, jako příslušný hospodařit s pozemkem p. č. KN 810 k. ú. Smiřice, okres Hradec Králové, nemá námitek k záměru "BESS k FVE SMIŘICE" v obci Smiřice, kat. území Smiřice, pozemek parc. č. 809/1.
Tedy na sousední nemovité věci, neboť z postoupených podkladů vyplývá, že předmětný pozemek nebude záměrem dotčen (mimo přesah ochranného pásma bateriového úložiště ve vzdálenosti menší než 2 m od hranice pozemku SPÚ).

Dále souhlasíme také se zbudováním nového sjezdu z pozemku č. 810 na předmětnou parcelu č. 809/1.

SPU 112224/2026/Soch, spuess9df58479
SZ SPU 110192/2026

„*elektronicky podepsáno*“

Ing. Petr Lázňovský
ředitel Krajského pozemkového úřadu
pro Královéhradecký kraj

POZNÁMKY

- PŘED ZAHÁJENÍM STAVBY INVESTOR SEZNÁMÍ ZHOTOVITELE SE VŠEMI SKUTEČNOSTMI, KTERÉ BY MOHLY MÍT VLIV NA STAVBU
- V PŘÍPADĚ ZJIŠTĚNÍ ODCHYLKY BUDE NEPRODLENĚ INFORMOVÁNA ZODPOVĚDNÁ OSOBA, KTERÁ STANOVÍ DALŠÍ POSTUP PRACÍ
- BUDOU DODRŽENY VZDÁLENOSTI APOD. DLE ZPRÁVY PBŘ!!!

S

ZODPOVĚDNÝ PROJEKTANT	Ing. Kateřina Šestáková Haucková, ČKAIT 0601789 Zlíč 73, 552 03 Česká Skalice			
VYPRACOVALA	ING. PAVLA JANEČKOVÁ			
INVESTOR	BESS Smiřice s.r.o. V Šáreckém údolí 764/1, Dejvice, 160 00 Praha			
ČÁST	C – SITUACE	Č. REVIZE	00	
NÁZEV AKCE	DOKUMENTACE PRO POVOLENÍ STAVBY BESS k FVE Smiřice parc. č. 809/1, k. ú. Smiřice	STUPEŇ	DSP	
		DATUM	3/2025	
NÁZEV VÝKRESU	KOORDINAČNÍ SITUAČNÍ VÝKRES–SOUHLAS	FORMÁT	MĚŘÍTKO	Č. VÝKRESU
		4xA4	1:500	C.3