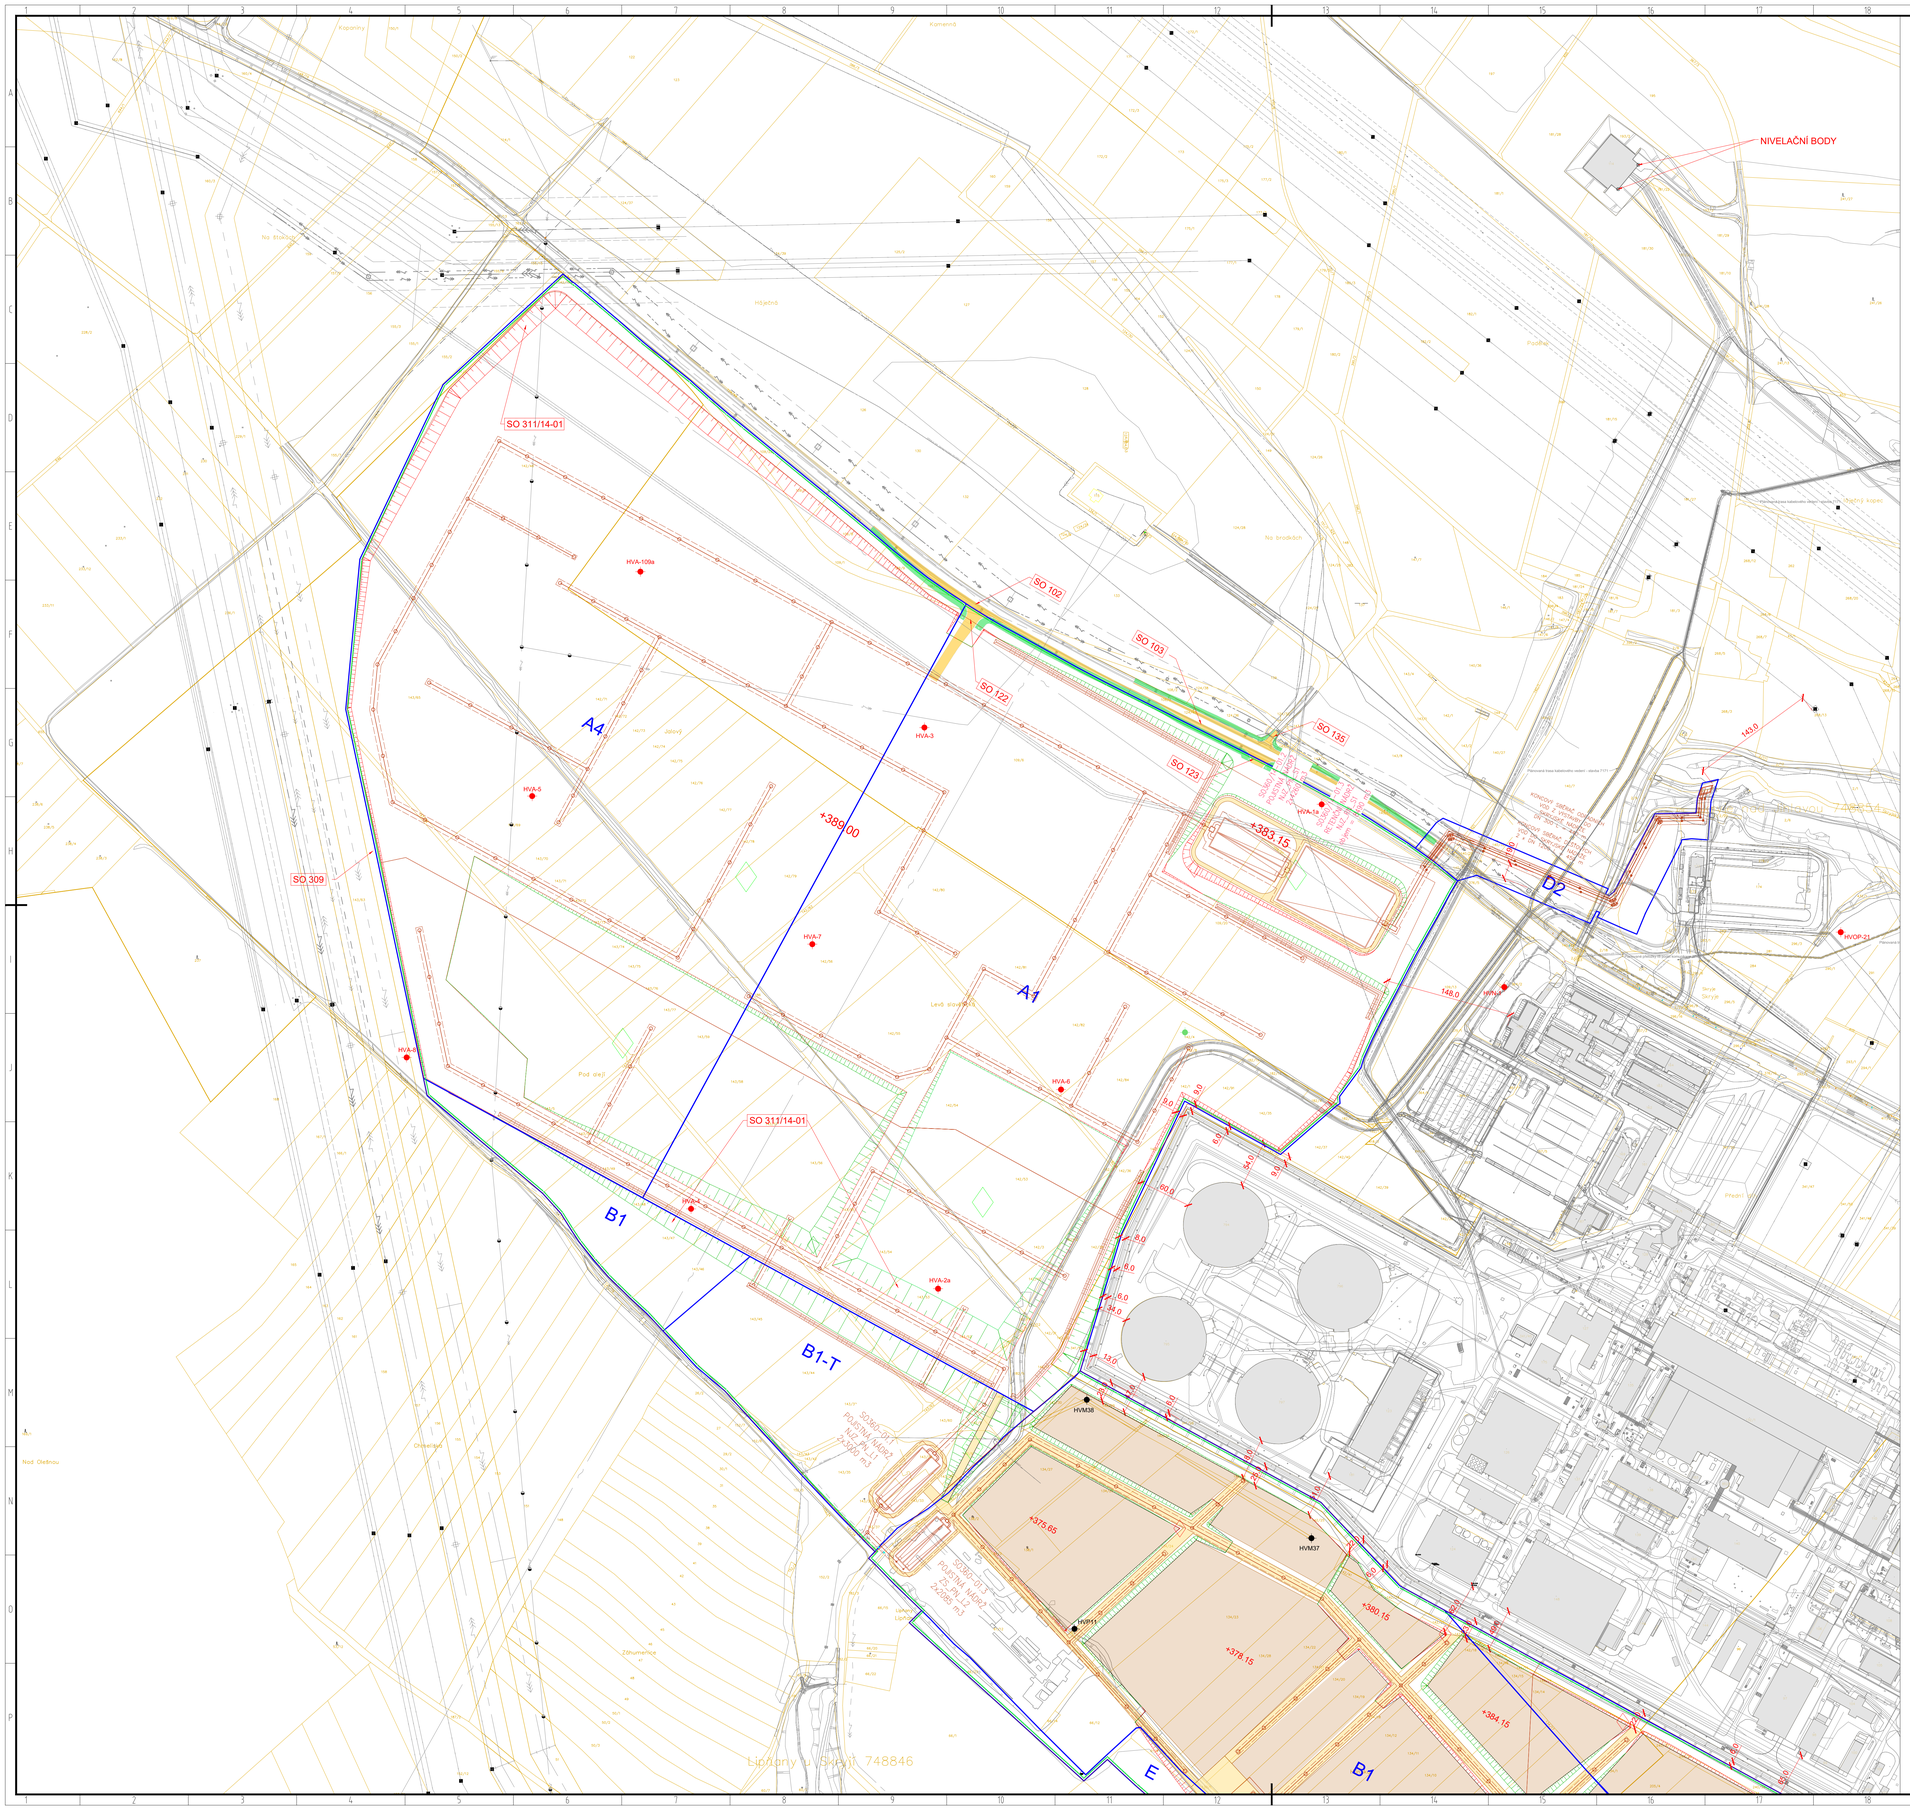


LEGENDA

hranice parcely

Dotčené plochy

Plocha A1	výstavba EDU5
Plocha A4	výstavba EDU6
Plocha B1	ZS
Plocha B3	ZS
Plocha D2	plocha odvedení odpadních vod a srážkových vod - Skryjský potok a VN Mohelno
Plocha E	ZS

Navržené stavební objekty

výkopy / násypy — SO 311/14-01 Hrubé terénní úpravy na výstavbové ploše

SO 311/15-01 Hrubé terénní úpravy na ploše ZS

SO 309 hranice Sejmutí ornice

Napojení stavby na technickou infrastrukturu

Navrhované komunikace a zpevněné plochy, napojení na dopravní infrastrukturu a úpravy silnic

SO 102, 103 Úprava silnice II/152

SO 111, 112, 113 Úprava silnice III/15249

SO 122, 123 Napojení účelové komunikace na sil. II/152

SO 131, 132, 133 Napojení účelové komunikace na sil. III/15249

SO 134, 141 Úprava napojení účelové komunikace na sil. III/15249 a úprava stávajících sjezdů

SO 135 Úprava napojení účelové komunikace na sil. II152

Doprovodná zeleň u komunikací

SO 360 vodohospodářské objekty

SO 360 ochranná pásma

hranice odvodňovaných ploch

SO 309/15-01 Zařízení staveniště pro přípravné práce

SO 309/15-02 Zpevněné plochy

SO 309/15-02 Staveništní komunikace

Přeložky technické infrastruktury v rámci jiných staveb

přeložka vedení 2x110kV V5584/5585

projektované V439/V440
projektované V436/V834

chráničky HDPE 40/33
22-NAZXS(F)2Y 3x1x240

Stávající technická infrastruktura

IS_ČEZ_Typy čar a mapových značek podle standardu ČEZ_ST_REV08

Kabelový kanál 350-1-01_ČEZ

Elektro - silnoproud - NN - neověřený průběh - Nefunkční kabel ČOV-Sokolovna_ČEZ

Elektro - silnoproud - NN - neověřený průběh - Pozůstatky kabelláže VO_ČEZ

Elektro - slaboproud - podzemní vedení - Dispečerské kabely EDU-RSLV - Trasa 1_ČEZ

Elektro - slaboproud - podzemní vedení - Dispečerské kabely EDU-RSLV_ČEZ

Elektro - slaboproud - podzemní vedení - Sdělovací kabel Dukovany - Elektrárna Mohelno_ČEZ

Elektro - slaboproud - neověřený průběh - Kabel ČOV-Stanička RK 352-1-03_ČEZ

Elektro - slaboproud - neověřený průběh - Kabel EDU - Meteostanice_ČEZ

Elektro - slaboproud - neověřený průběh - Kabely SKŘ z ČOV do SOV_ČEZ

Elektro - slaboproud - neověřený průběh - Kabely SKŘ RK ze SOV na DRK1_ČEZ

Elektro - silnoproud - NN - neověřený průběh - Venkovní osvětlení ČOV 352-01-03_ČEZ

Elektro - veřejné osvětlení - neověřený průběh - Venkovní osvětlení ČOV_ČEZ

Elektro - silnoproud - VN - podzemní vedení - Napájení Areálu ČOV_ČEZ

Elektro - silnoproud - VN - neověřený průběh - Vedení 22kV mezi PVE Dalešice a Elektrárnou Moheln VN817_ČEZ

Kanalizace - dešťová - podzemní vedení - Dešťová kanalizace odtok do vodoteče Rokytná 360-1-11_ČEZ

Kanalizace - dešťová - podzemní vedení - Dešťová kanalizace směr ČOV vč. Šachet_ČEZ

Kanalizace - dešťová - neověřený průběh - _Dešťová kanalizace odtok do vodoteče Rokytná 360-1-11_ČEZ

Kanalizace - dešťová - neověřený průběh - Dešťová kanalizace směr ČOV vč. Šachet_ČEZ

Kanalizace - dešťová - neověřený průběh - Výsledná kanalizace dešťové vody_ČEZ

Kanalizace - dešťová - neověřený průběh -Dešťová kanalizace z KORDů podél_ČEZ

Kanalizace - splašková - podzemní vedení - Splašková kanalizace směr areál Heřmanice_ČEZ

Kanalizace - splašková - neověřený průběh - Výsledná kanalizace splaškové vody_ČEZ

Kanalizace - drenážní - podzemní vedení - Meliorace_ČEZ

Voda - pitná - neověřený průběh - Přípojka pitné vody EDU - ČS Jihlava_ČEZ

Voda - pitná - neověřený průběh - Přípojka pitné vody pro COV a SOV_ČEZ

Voda - pitná - neověřený průběh - Přípojka pitné vody pro EDU1-4_ČEZ

Voda - pitná - neověřený průběh - Přípojka pitné vody pro KORDY_ČEZ

Voda - pitná - neověřený průběh - Rezervní nepoužívaný vodovodní řad DN125_ČEZ

Voda - požární - neověřený průběh - Požární vodovod_ČEZ

Voda - surová - podzemní vedení - Přívody surové vody do EDU_ČEZ

Voda - surová - podzemní vedení_M05c Rezervní nepoužívaný řad surové vody_ČEZ

HVA-109a — Monitorovací vrty u EDU1-4

HVA-109a — Monitorovací vrty v okolí NJZ EDU

odběrové místo půdy areál NJZ EDU (8)

Poznámky:
Vyznačení jednotlivých navržených nebo odstraňovaných staveb a technické infrastruktury je na výkresu C.4 Demolice
Vyznačení požárně nebezpečných prostorů, přístupové komunikace pro požární techniku, nástupní plochy pro požární techniku, zdroje požární vody viz speciální výkres C.6_ZOV

IS vyjádření podle provozovatelů

Cetin - neprovozované sítě

Cetin - Sítě s NN, elektropřípojky

Cetin - Sítě s NN, elektropřípojky ochranné pásmo 1 m

Cetin - Zaměřené a kótované, vnitřní sítě - optické + souběh

Enecos - Zaměřené a kótované, vnitřní sítě - optické + souběh

Paprsek směrového radioreléového spoje veřejné komunikační sítě Českých Radiokomunikací

EGD

VAS, a.s. divize Třebíč - Vodovodní řad Slavětice - Dukovany

ČEPS - silnoproud - VVN - nadzemní vedení

ČEPS - silnoproud - VVN - ochranné pásmo

ČEZ ICT Services, a.s. - podzemní metalické vedení

Elektro - silnoproud - VN - Betonový stožár _ EON - vyjádření

Elektro - silnoproud - VVN - Příhradový stožár _ EON - vyjádření

Elektro - silnoproud - VVN - Příhradový stožár _ ČEPS - vyjádření

Elektro - silnoproud - VVN - Betonový stožár _ ČEPS - vyjádření

Digitálně podepsal Ing. arch. Petr Gregor
Datum: 2026.06.03 07:33:33 +02'00'

SOUŘADNICOVÝ SYSTÉM S-JTSK
VÝŠKOVÝ SYSTÉM - BALT p.v.

N
W E
S

ÚJV Řež, a. s.
Divize ENERGOPROJEKT PRAHA

Pracoviště: Na Žertvách 2247/29, 180 00 Praha 8
Ředící útvar: 2505 | Zpracovatelský útvar: 2530 | Skartační znak: A
Označení MP: 02 | Označení KP: 05 | Část dokumentace: C.3 | Objekt-Provozní soubor: | Pořadové číslo: 003
Označení ZL: 04/2025
Název zadání: Příprava výstavbové plochy a plochy zařízení staveniště
Název stavby: ZL - 04/2025
Název výkresu: **speciální situační výkres**
C.3 KOORDINAČNÍ SITUACE STAVBY - ČÁST PLOCHA VÝSTAVBY
Stupeň ochrany | Číslo stavby

Vypracoval: Ing.arch. Petr Gregor | Vedoucí zpracovatelského útvaru: Ing. Jan Stanislav | Datum: 06/2026 | Měřítko: 1 : 1000
Kontroloval: Ing. Jiří Šťastný | HIP: Ing. Jiří Kopta | Soubor: ZL-04_2025_C3_KOO_003 | Formát: A 0 / 16 x A4
Zakázkové číslo: 25-05806-30-004 | Archivní číslo projektu: 859-4-D-2025-0038 | Archivní číslo digitálního archivu: | Index: | List: 1

A0/16A4 (841x1189)