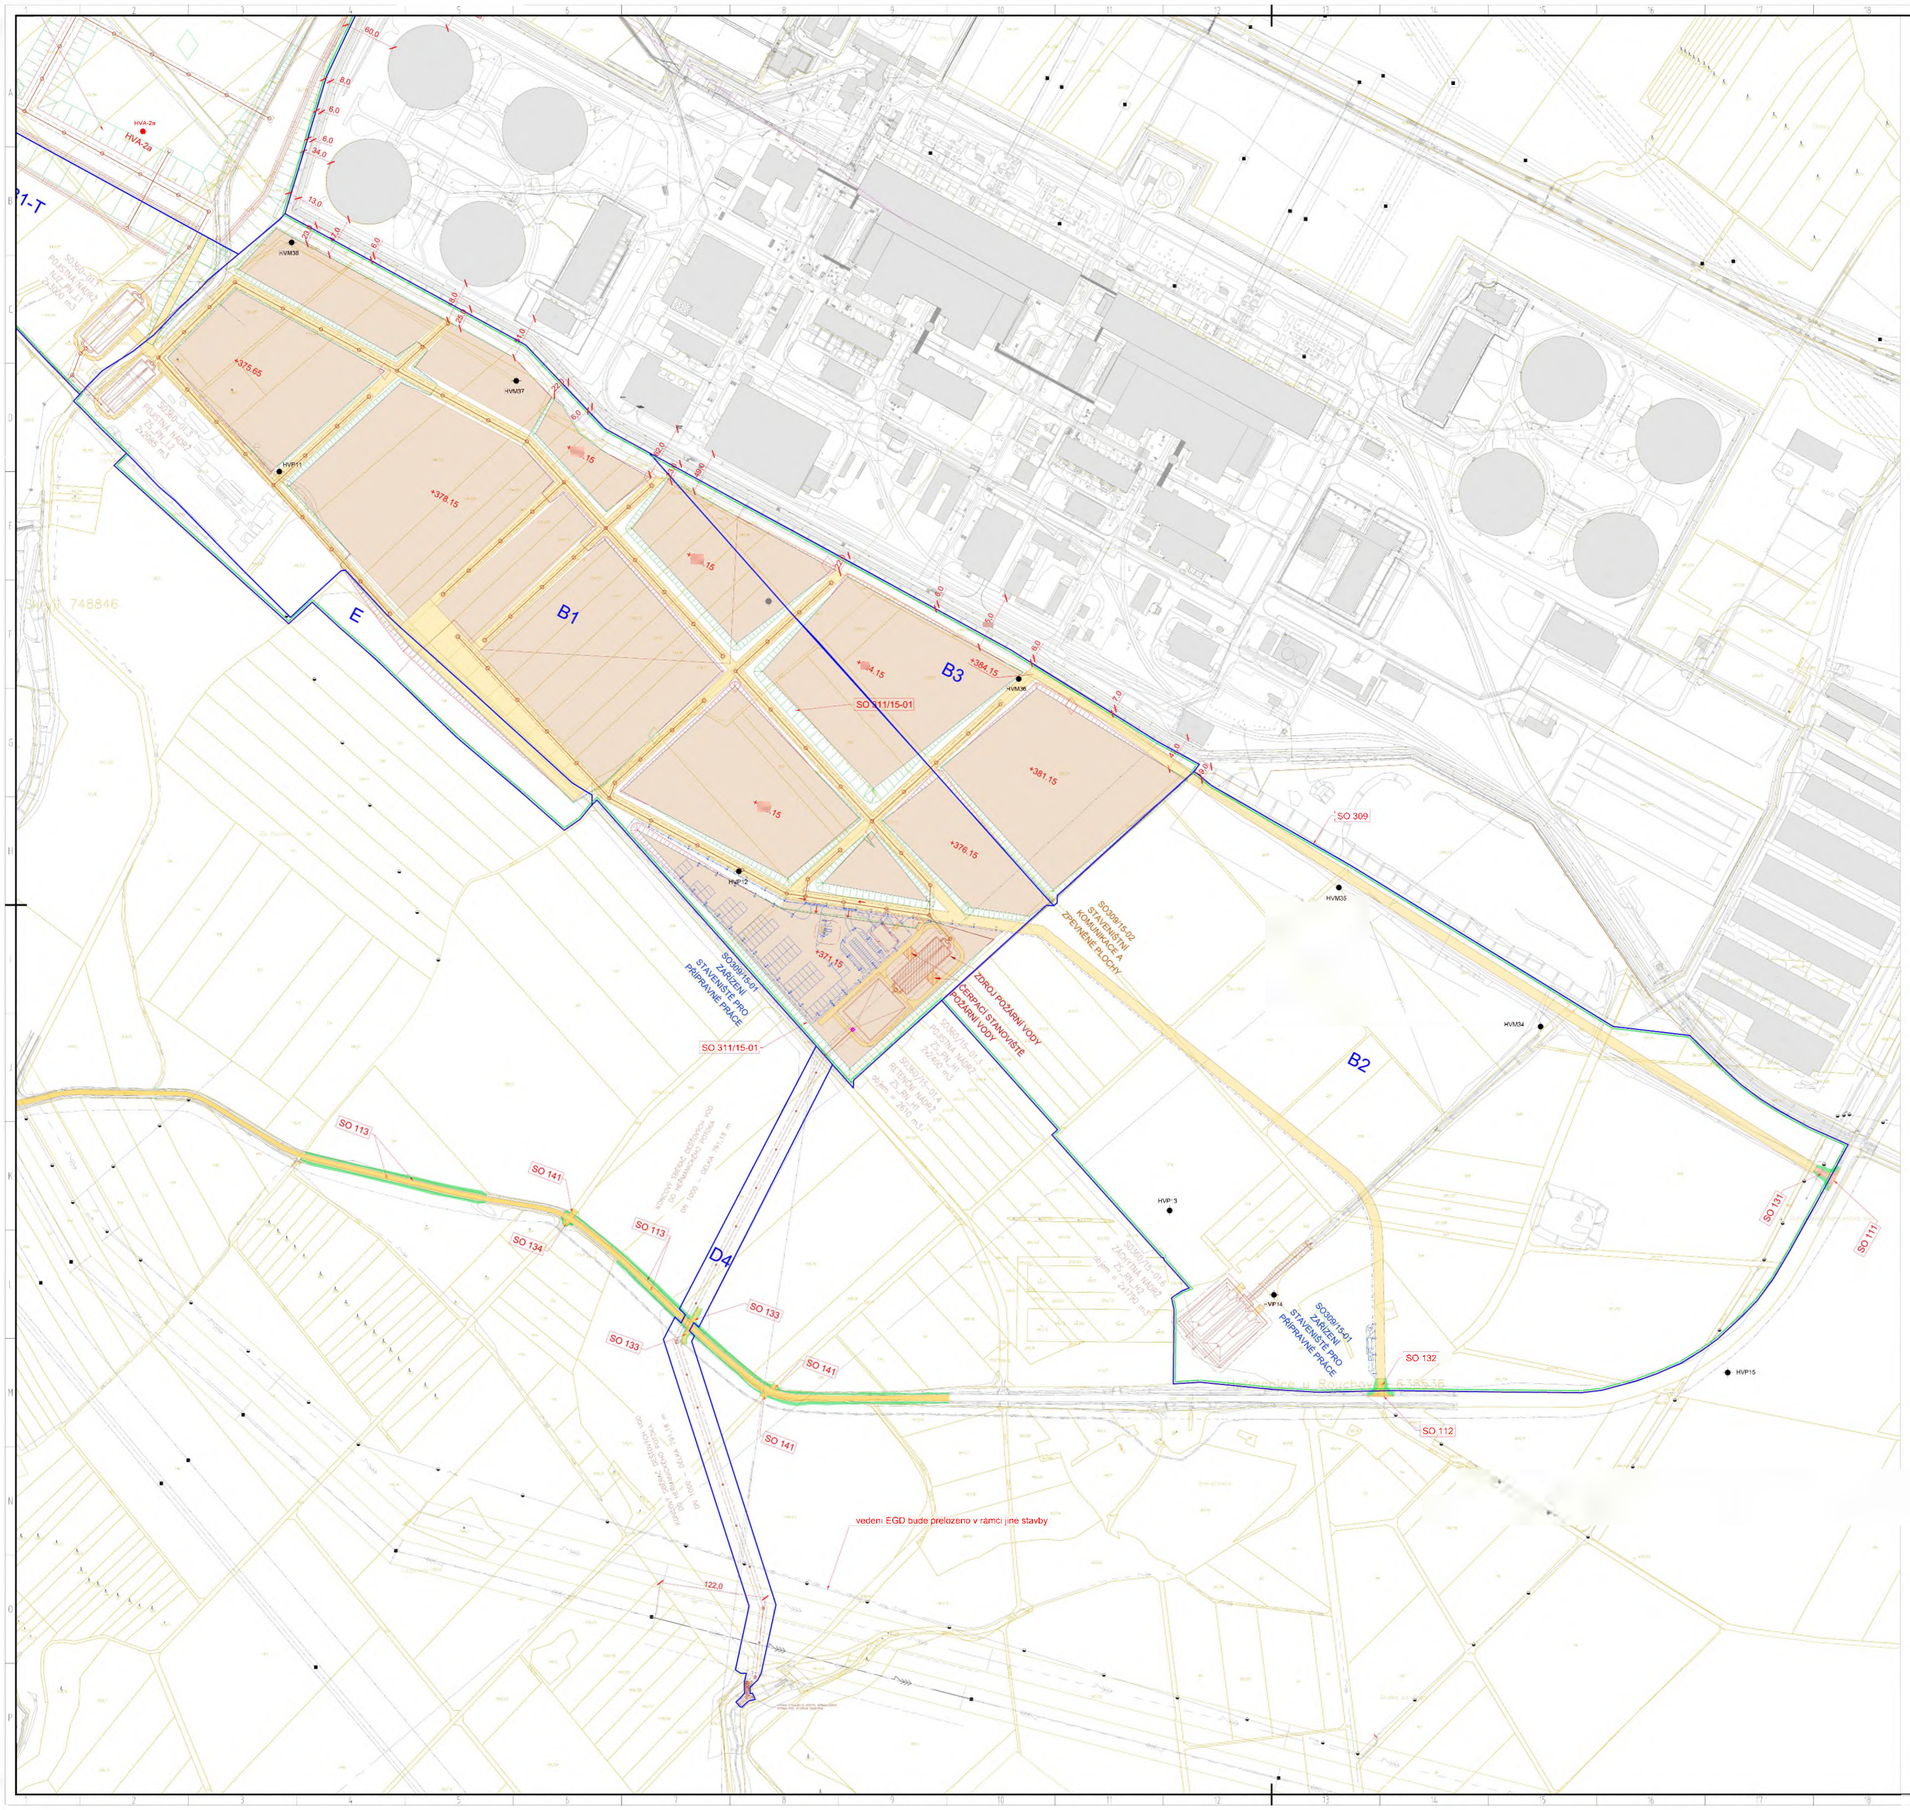


LEGENDA

hranice parcely

Dotčené plochy

Plocha B1
Plocha B2 deponie ornice/podorniči
Plocha B3 ZS
Plocha D4 plocha pozemků vyčleněných pro vypouštění srážkových vod - Helmanický potok
Plocha E ZS

požárně nebezpečný prostor
příjezd HZS

Navržené stavební objekty

výkopy násypy

SO 311/14-01 Hrubé terénní úpravy na výstavbové ploše
SO 311/15-01 Hrubé terénní úpravy na ploše ZS
SO 309 hranice Sejmutí ornice

Napojení stavby na technickou infrastrukturu

Navrhované komunikace a zpevněné plochy, napojení na dopravní infrastrukturu

SO 102, 103 **Úprava silnice II/152**
SO **111**, 112, 113 **Úprava silnice III/15245**
SO 122, 123 Napojení účelové komunikace na sil. II/152
SO 131, 132, 133 Napojení účelové komunikace na sil. III/15249
SO 134, 141 Úprava napojení účelové komunikace na sil. III/15249 a úprava stávajících sjezdů
SO 135 Úprava napojení účelové komunikace na sil. II/152
Doprovodná zeleň u komunikací

SO 360 vodohospodářské objekty
SO 360 ochranná pásma
hranice odvodňovaných ploch

SO 309/15-01 Zařízení staveniště pro přípravné práce
SO 309/15-02 Zpevněné plochy
SO 309/15-02 Staveništní komunikace

Přeložky technické infrastruktury v rámci jiných staveb

přeložka vedení 2x110kV V5584/5585 — projektované V439/V440, projektované V436/V834

chrániček HDPE 40/33 22-NA2XS(F)2Y 3x1x240

Stávající technická infrastruktura

IS_ČEZ_Typy čar a mapových značek podle standardu ČEZ_ST_REV08

Kabelový kanál 350-1-01_ČEZ
Elektro - silnoproud - NN - neověřený průběh - Nefunkční kabel COV-Sokolovna_ČEZ
Elektro - silnoproud - NN - neověřený průběh - Pozůstatky kabelláže VO_ČEZ
Elektro - slaboproud - podzemní vedení - Dispečerské kabely EDU-RSLV - Trasa 1_ČEZ
Elektro - slaboproud - podzemní vedení - Dispečerské kabely EDU-RSLV_ČEZ
Elektro - slaboproud - podzemní vedení - Sdělovací kabel Dukovany - Elektrárna Mohelno_ČEZ
Elektro - slaboproud - neověřený průběh - Kabel ČOV-Stanička RK 352-1-03_ČEZ
Elektro - slaboproud - neověřený průběh - Kabel EDU - Meteostanice_ČEZ
Elektro - slaboproud - neověřený průběh - Kabely SKŘ z ČOV do SOV_ČEZ
Elektro - slaboproud - neověřený průběh - Kabely SKŘ RK ze SOV na DRK1_ČEZ
Elektro - silnoproud - NN - neověřený průběh - Venkovní osvětlení ČOV 352-01-03_ČEZ
Elektro - veřejné osvětlení - neověřený průběh - Venkovní osvětlení ČOV_ČEZ
Elektro - silnoproud - VN - podzemní vedení - Napájení Areálu ČOV_ČEZ
Elektro - silnoproud - VN - neověřený průběh - Vedení 22kV mezi PVE Dalešice a Elektrárnou Mohelno VN817_ČEZ
Kanalizace - dešťová - podzemní vedení - Dešťová kanalizace odtok do vodoteče Rokytná 360-1-11_ČEZ
Kanalizace - dešťová - podzemní vedení - Dešťová kanalizace směr ČOV vč. Šachet_ČEZ
Kanalizace - dešťová - neověřený průběh - _Dešťová kanalizace odtok do vodoteče Rokytná 360-1-11_ČEZ
Kanalizace - dešťová - neověřený průběh - Dešťová kanalizace směr ČOV vč. Šachet_ČEZ
Kanalizace - dešťová - neověřený průběh - Výsledná kanalizace dešťové vody_ČEZ
Kanalizace - dešťová - neověřený průběh -Dešťová kanalizace z KORIDu podél_ČEZ
Kanalizace - splašková - podzemní vedení - Splašková kanalizace směr areál Heřmanice_ČEZ
Kanalizace - splašková - neověřený průběh - Výsledná kanalizace splaškové vody_ČEZ
Kanalizace - drenážní - podzemní vedení - Meliorace_ČEZ
Voda - pitná - neověřený průběh - Přípojka pitné vody EDU - ČS Jihlava_ČEZ
Voda - pitná - neověřený průběh - Přípojka pitné vody pro ČOV a SOV_ČEZ
Voda - pitná - neověřený průběh - Přípojka pitné vody pro EDU1+4_ČEZ
Voda - pitná - neověřený průběh - Přípojka pitné vody pro KORDY_ČEZ
Voda - pitná - neověřený průběh - Rezervní nepoužívaný vodovodní řad DN125_ČEZ
Voda - požární - neověřený průběh - Požární vodovod_ČEZ
Voda - surová - podzemní vedení - Přívody surové vody do EDU_ČEZ
Voda - surová - podzemní vedení_M56c Rezervní nepoužívaný řad surové vody_ČEZ
HVA-109x HVA-108x Monitorovací vrty u EDU1-4
Monitorovací vrty v okolí NJZ EDU

Poznámky:

Vyznačení jednotlivých navržených nebo odstraňovaných staveb a technické infrastruktury je na výkresu C.4 Demolice

Vyznačení požárně nebezpečných prostorů, přístupové komunikace pro požární techniku, nástupní plochy pro požární techniku, zdroje požární vody viz speciální výkres C.6_ZOV

IS vyjádření podle provozovatelů

Cetin - neprovozované sítě
Cetin - Sítě s NN, elektropřípojky
Cetin - Sítě s NN, elektropřípojky ochranná pásmo 1 m
Cetin - Zaměřené a kótované, vnitřní sítě - optické + souběh
Enecos - Zaměřené a kótované, vnitřní sítě - optické + souběh
Paprsek směrového radioreléového spoje veřejné komunikační sítě Českých Radiokomunikací
EGD
VAS, a.s. divize Třebíč - Vodovodní řad Slavětice - Dukovany
ČEPS - silnoproud - VVN - nadzemní vedení
ČEPS - silnoproud - VVN - ochranné pásmo
ČEZ ICT Services, a.s. - podzemní metalické vedení
Elektro - silnoproud - VN - Betonový stožár _ EON - vyjádření
Elektro - silnoproud - VVN - Příhradový stožár _ EON - vyjádření
Elektro - silnoproud - VVN - Příhradový stožár _ ČEPS - vyjádření
Elektro - silnoproud - VVN - Betonový stožár _ ČEPS - vyjádření

Digitálně podepsal Ing. arch. Petr Gregor
Datum: 2026.06.03 07:35:52 +02'00'

SOUŘADNICOVÝ SYSTÉM S-JTSK
VÝŠKOVÝ SYSTÉM - BALT p.v.

N

ÚJV Řež, a. s.
Divize 30 ENERGOPROJEKT PRAHA

speciální situační výkres
C.3 KOORDINAČNÍ SITUACE STAVBY - ČÁST PLOCHA ZAŘÍZENÍ STAVENIŠTĚ

859-4-D-2025-0038