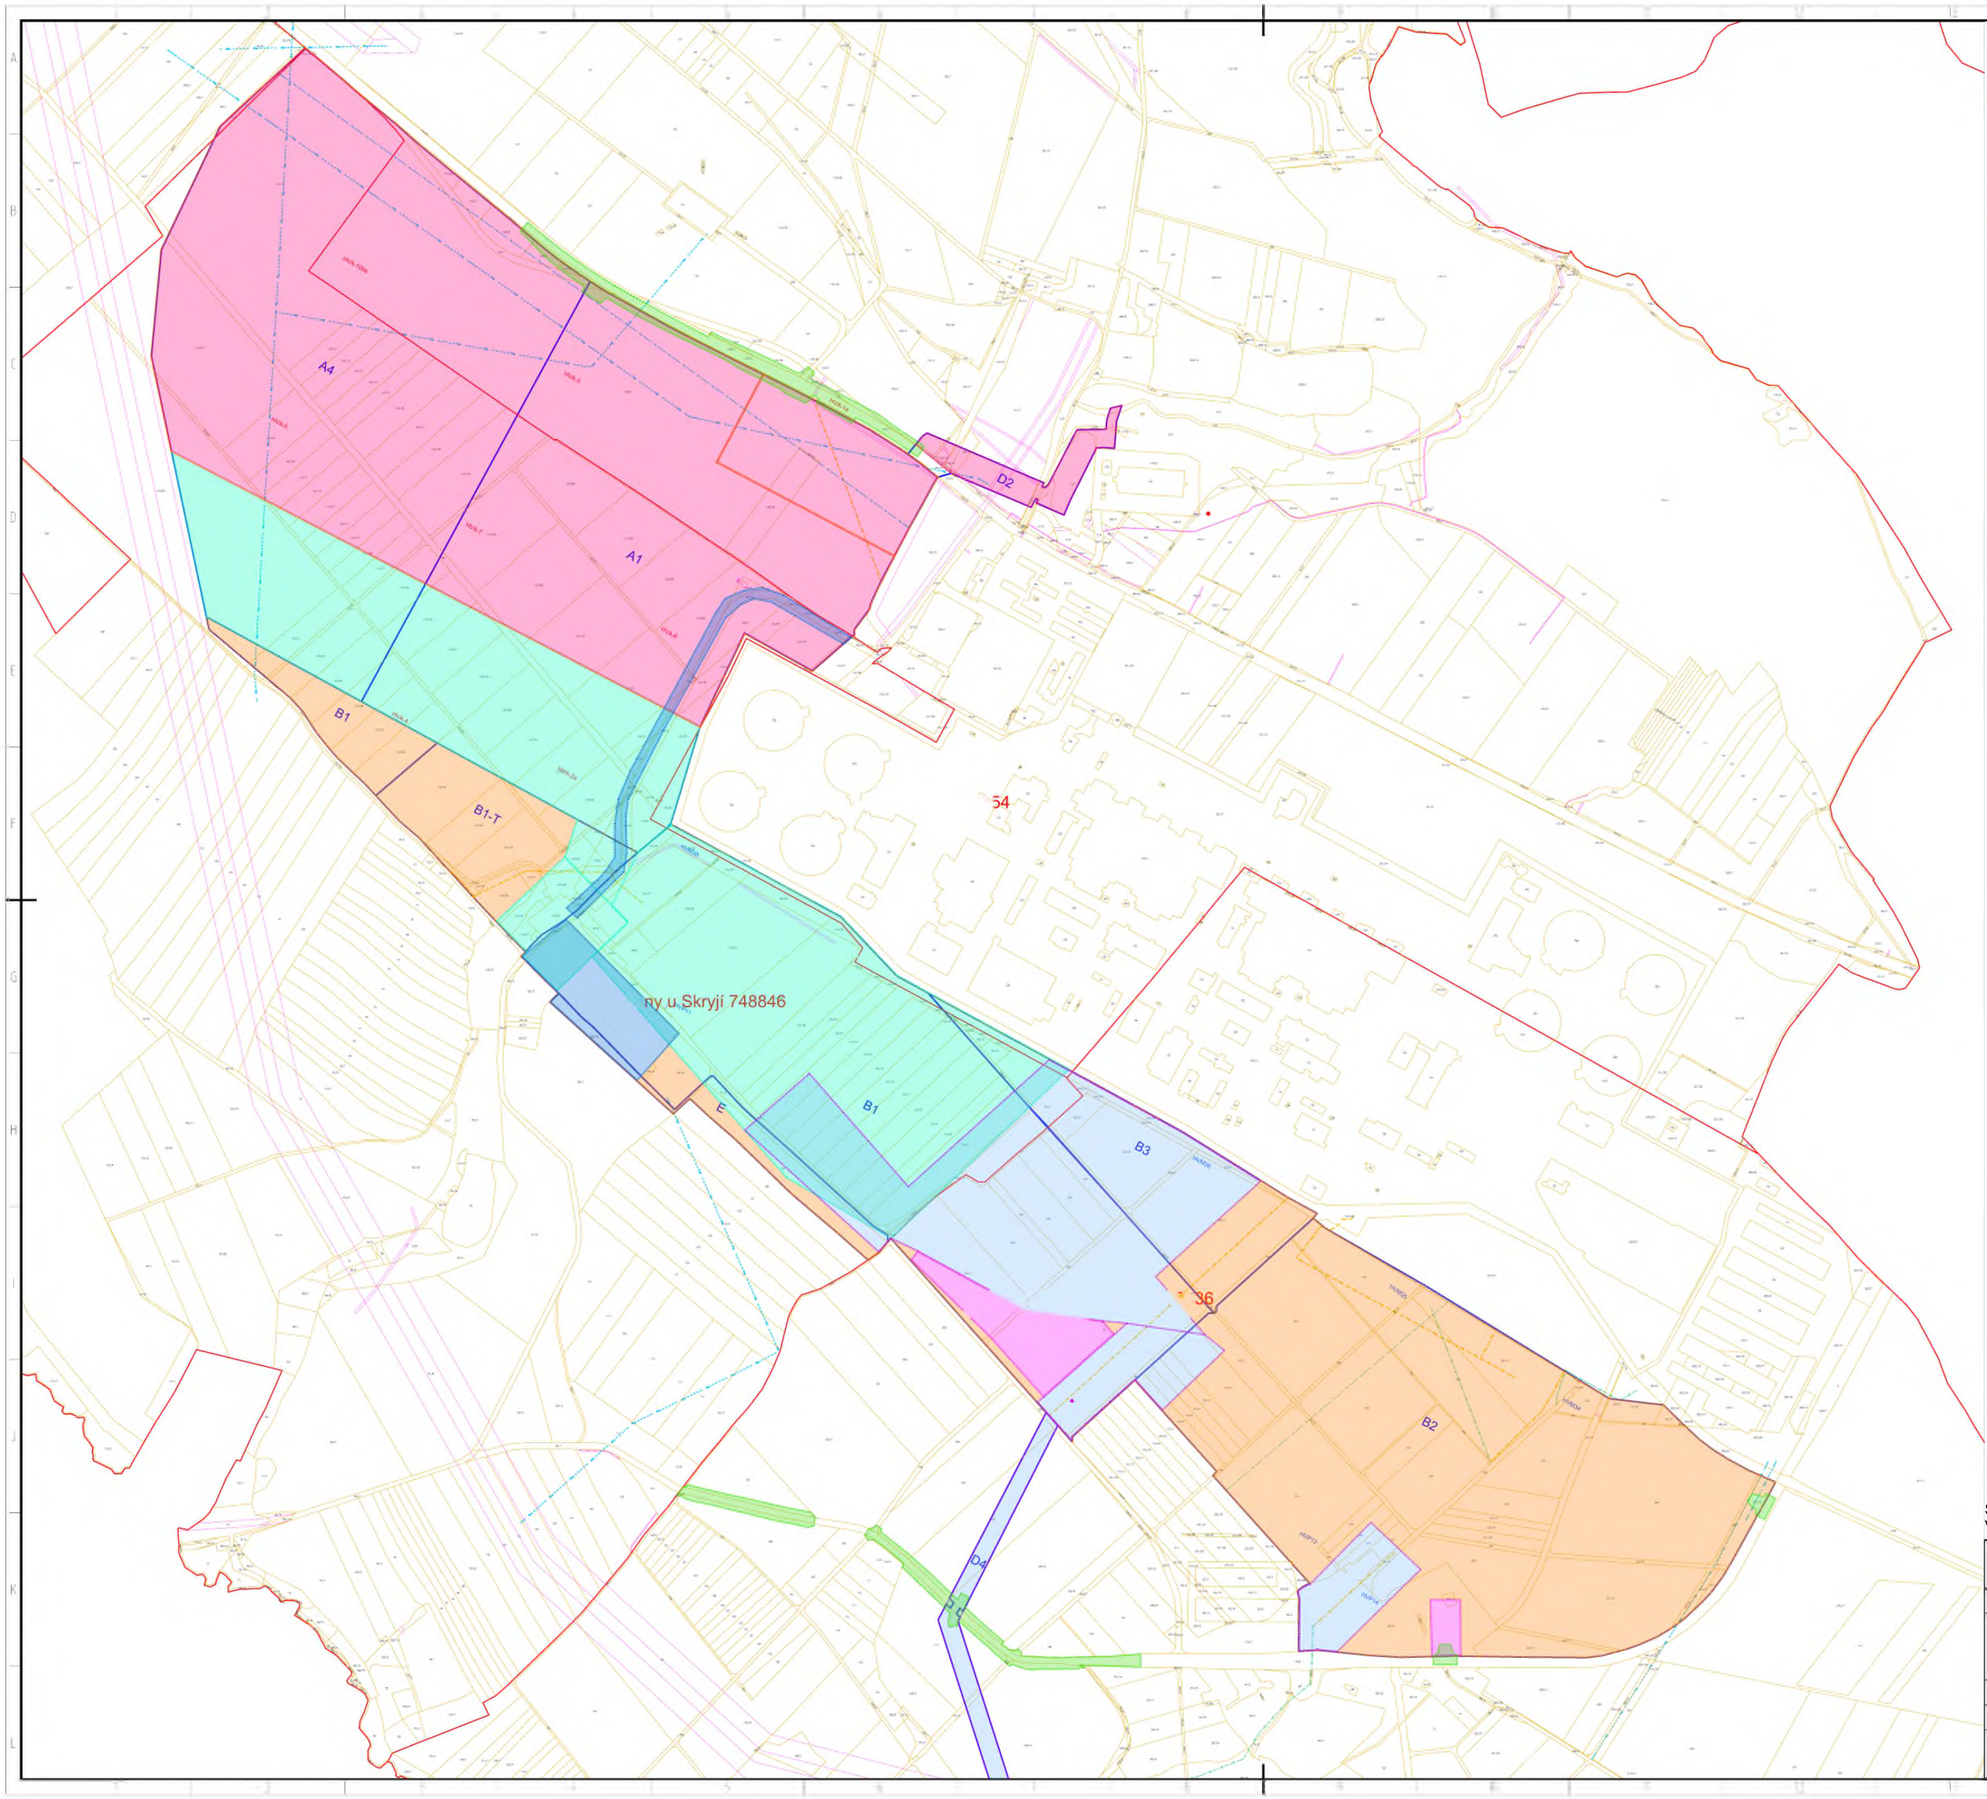


LEGENDA

- staveniště stavby S-1
- staveniště stavby S-2
- staveniště stavby S-3
- staveniště stavby S-4
- staveniště stavby S-5 a S-6
- staveniště stavby S-7
- staveniště stavby S-8

Soubor staveb je složen stavbami:

Stavba S-1	Přípravné práce
Stavba S-2	Zařízení staveniště pro přípravné práce
Stavba S-3	Pojistné nádrže pro odvedení srážkových vod z ploch NJZ EDU a ZS Lipňanským potokem
Stavba S-4	Odvedení srážkových vod z ploch zařízení staveniště NJZ EDU do Heřmanického potoka
Stavba S-5	Odvedení srážkových vod z plochy NJZ EDU do Skryjské nádrže
Stavba S-6	Odvedení odpadních vod z výstavby NJZ EDU do Skryjské nádrže
Stavba S-7	Napojení NJZ EDU na dopravní infrastrukturu a úpravu silnic
Stavba S-8	Demolice

Dotčené plochy

Plocha A1	výstavba EDU5
Plocha A4	výstavba EDU6
Plocha B1	ZS
Plocha B2	deponie ornice/podorniční
Plocha B3	ZS
Plocha D2	plocha odvedení odpadních vod a srážkových vod - Skryjský potok a VN Mohelno
Plocha D4	plocha pozemků vyčleněných pro vypouštění srážkových vod - Heřmanický potok
Plocha E	ZS

- hranice parcely
- hranice katastrálního území
- hranice věcných břemen

N

W E

S

SOUŘADNICOVÝ SYSTÉM S-JTSK
VÝŠKOVÝ SYSTÉM - BALT p.v.

Ing. arch. PETR GREGOR autorizovaný inženýr pro pozemní stavby a urbanismus ČKAIT - 0011636

Digitálně podepsal Ing. arch. Petr Gregor
Datum: 2026.06.03 07:55:12 +02'00'

ÚJV Řež, a. s.
Divize 42 ENERGOPROJEKT PRAHA

speciální situační výkres
C.4 SITUACE ZÁBORŮ

859-4-D-2025-0042