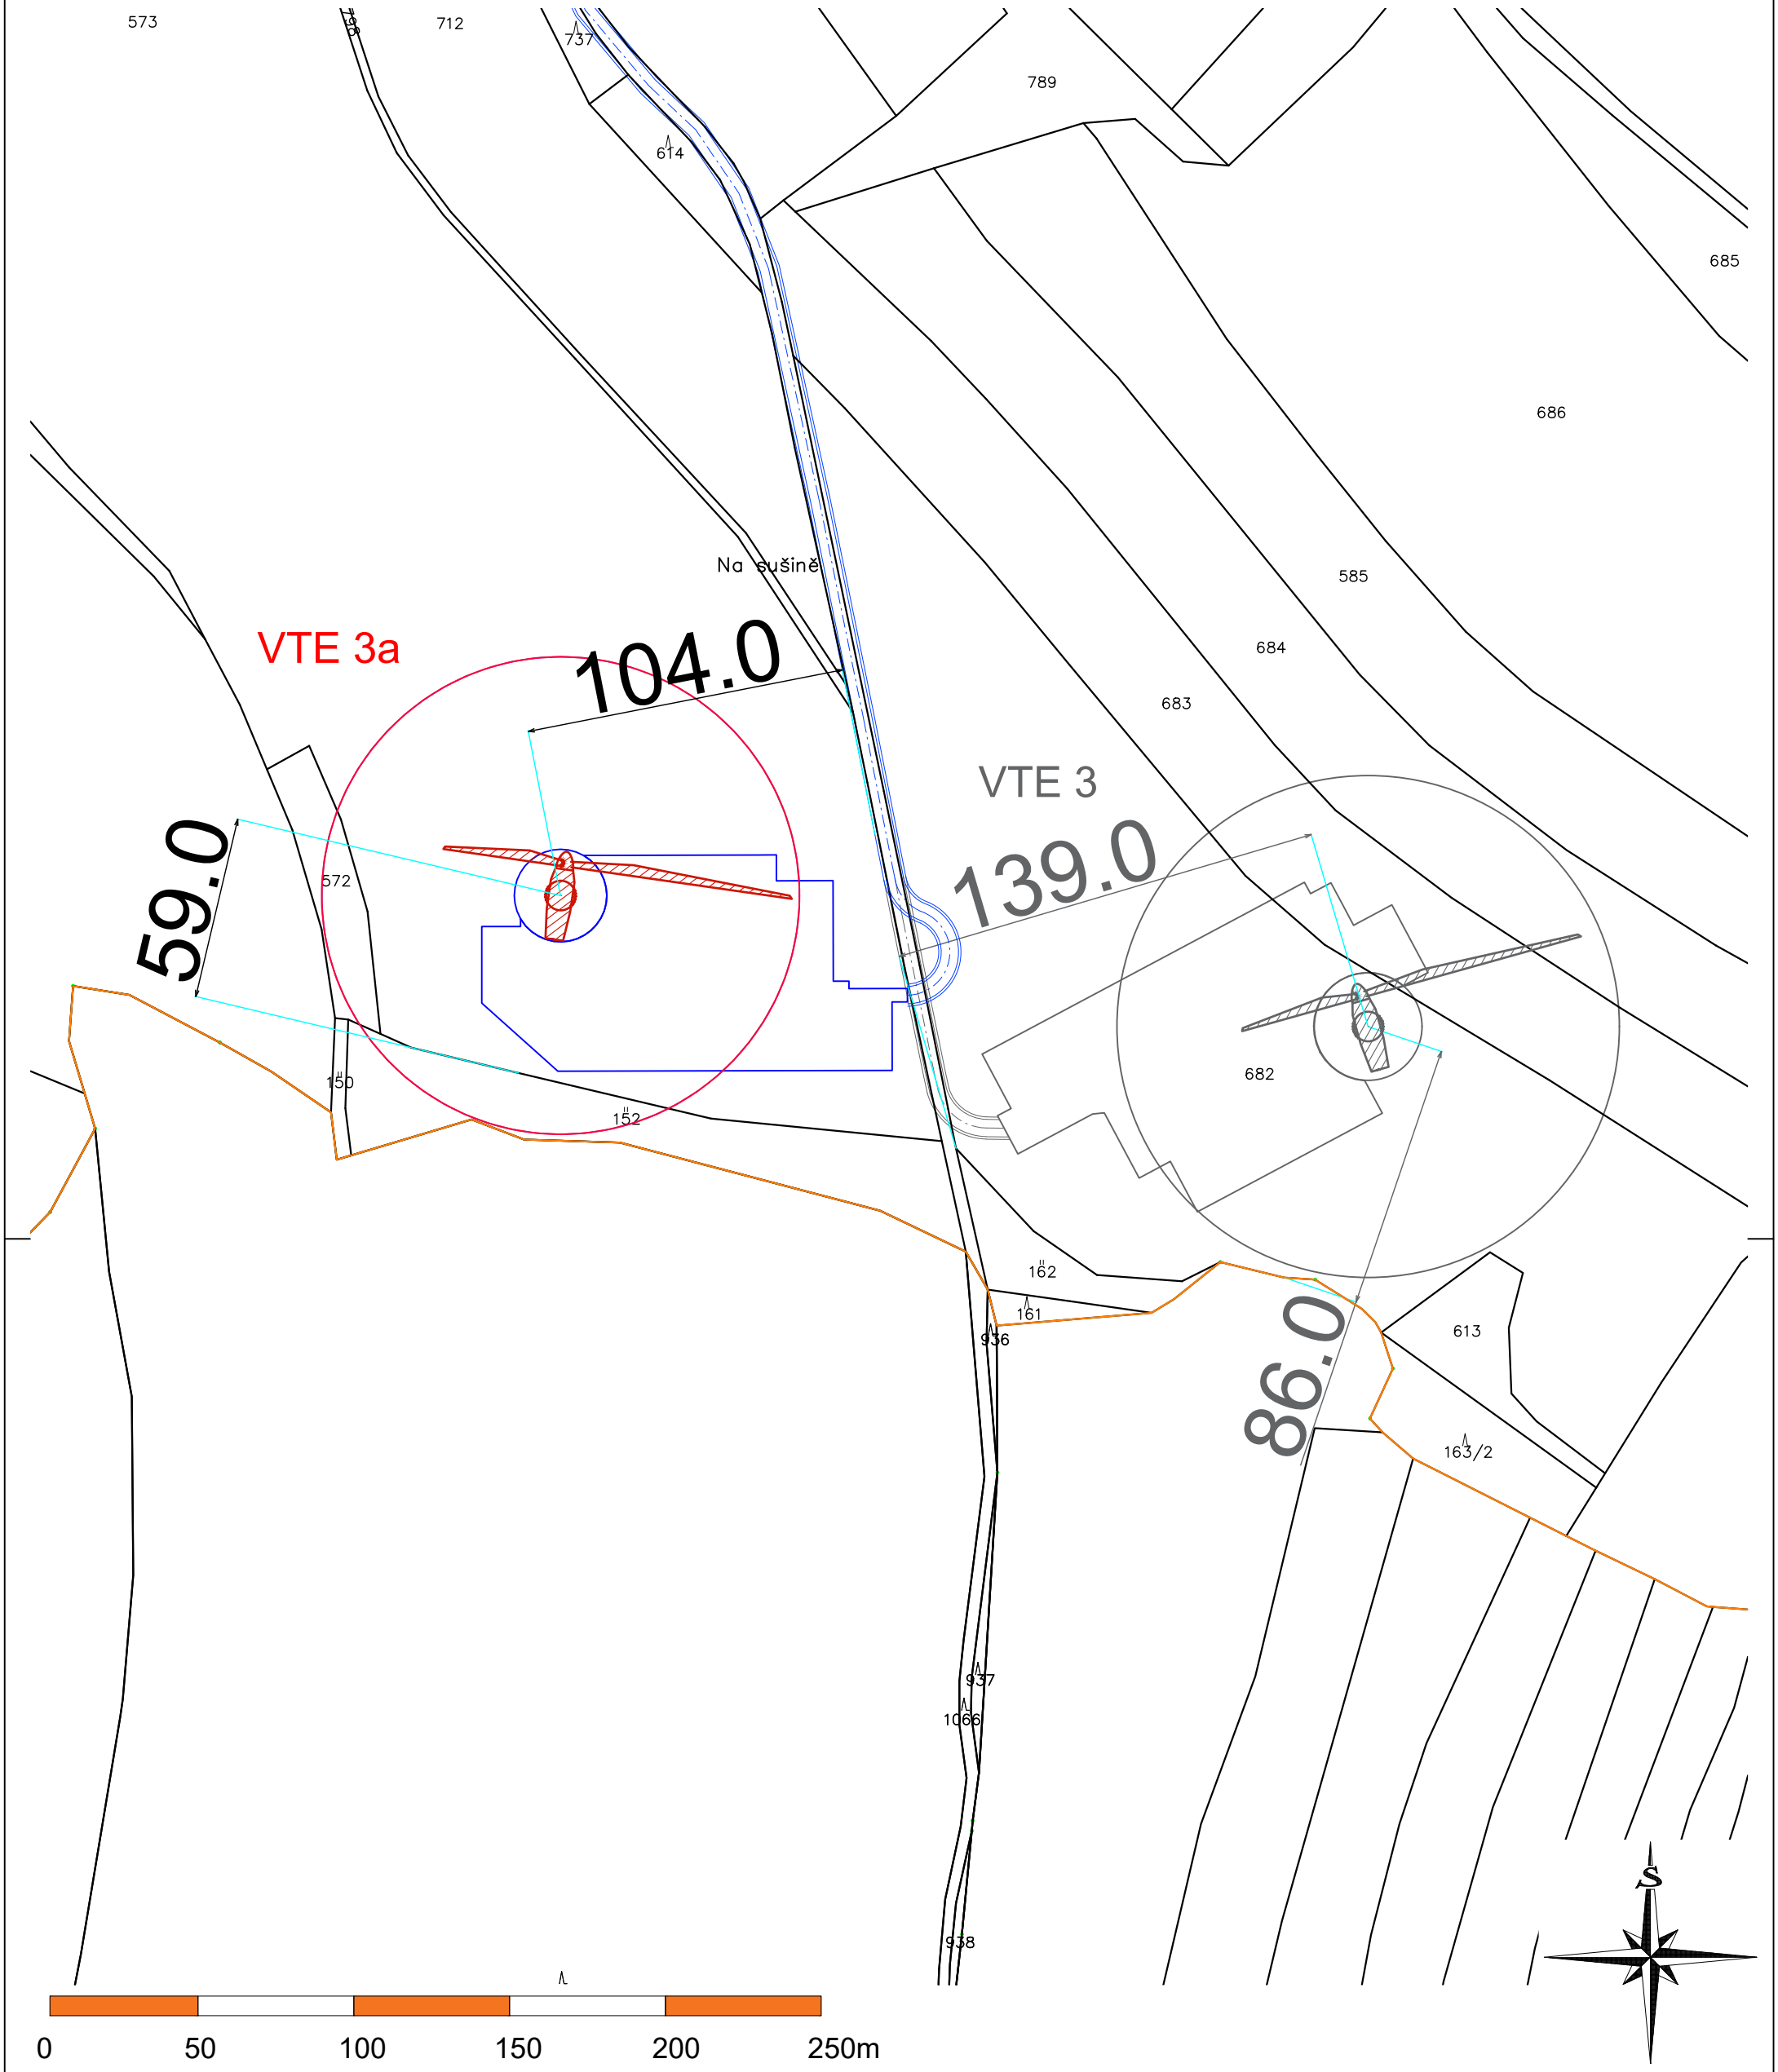


LEGENDA:

- Navržená větrná elektrárna
- Manipulační plocha a zařízení staveniště
- Alternativní pozice VTE
- Přístupová komunikace
- Bezpečnostní pásmo plynovodu - VTL
- Ochranné pásmo VTL plynovodu
- Sdělovací vedení metalické
- VTL Plynovod - podzemní
- Sdělovací vedení optické
- Osa přístupové komunikace


Vypracoval:	Schválil:
Ing. David Havlíček	Jakub Hejna

ČEZ Obnovitelné zdroje, s.r.o.
Duhová 1444 / 2
Praha 4 - Michle 140 00

Investor:	ČEZ, a. s.
Název stavby:	**VTE Šlapanov**
Objekt (SO), provozní celek (PC):	VTE Šlapanov
Obsah výkresu:	**Katastrální situační výkres**

Datum:	03/2026
Stupeň dokumentace:	Studie
Měřítko:	1:2000
Formát:	A3
Revize:	
Číslo stavby:	-
Číslo výkresu:	Paré

03

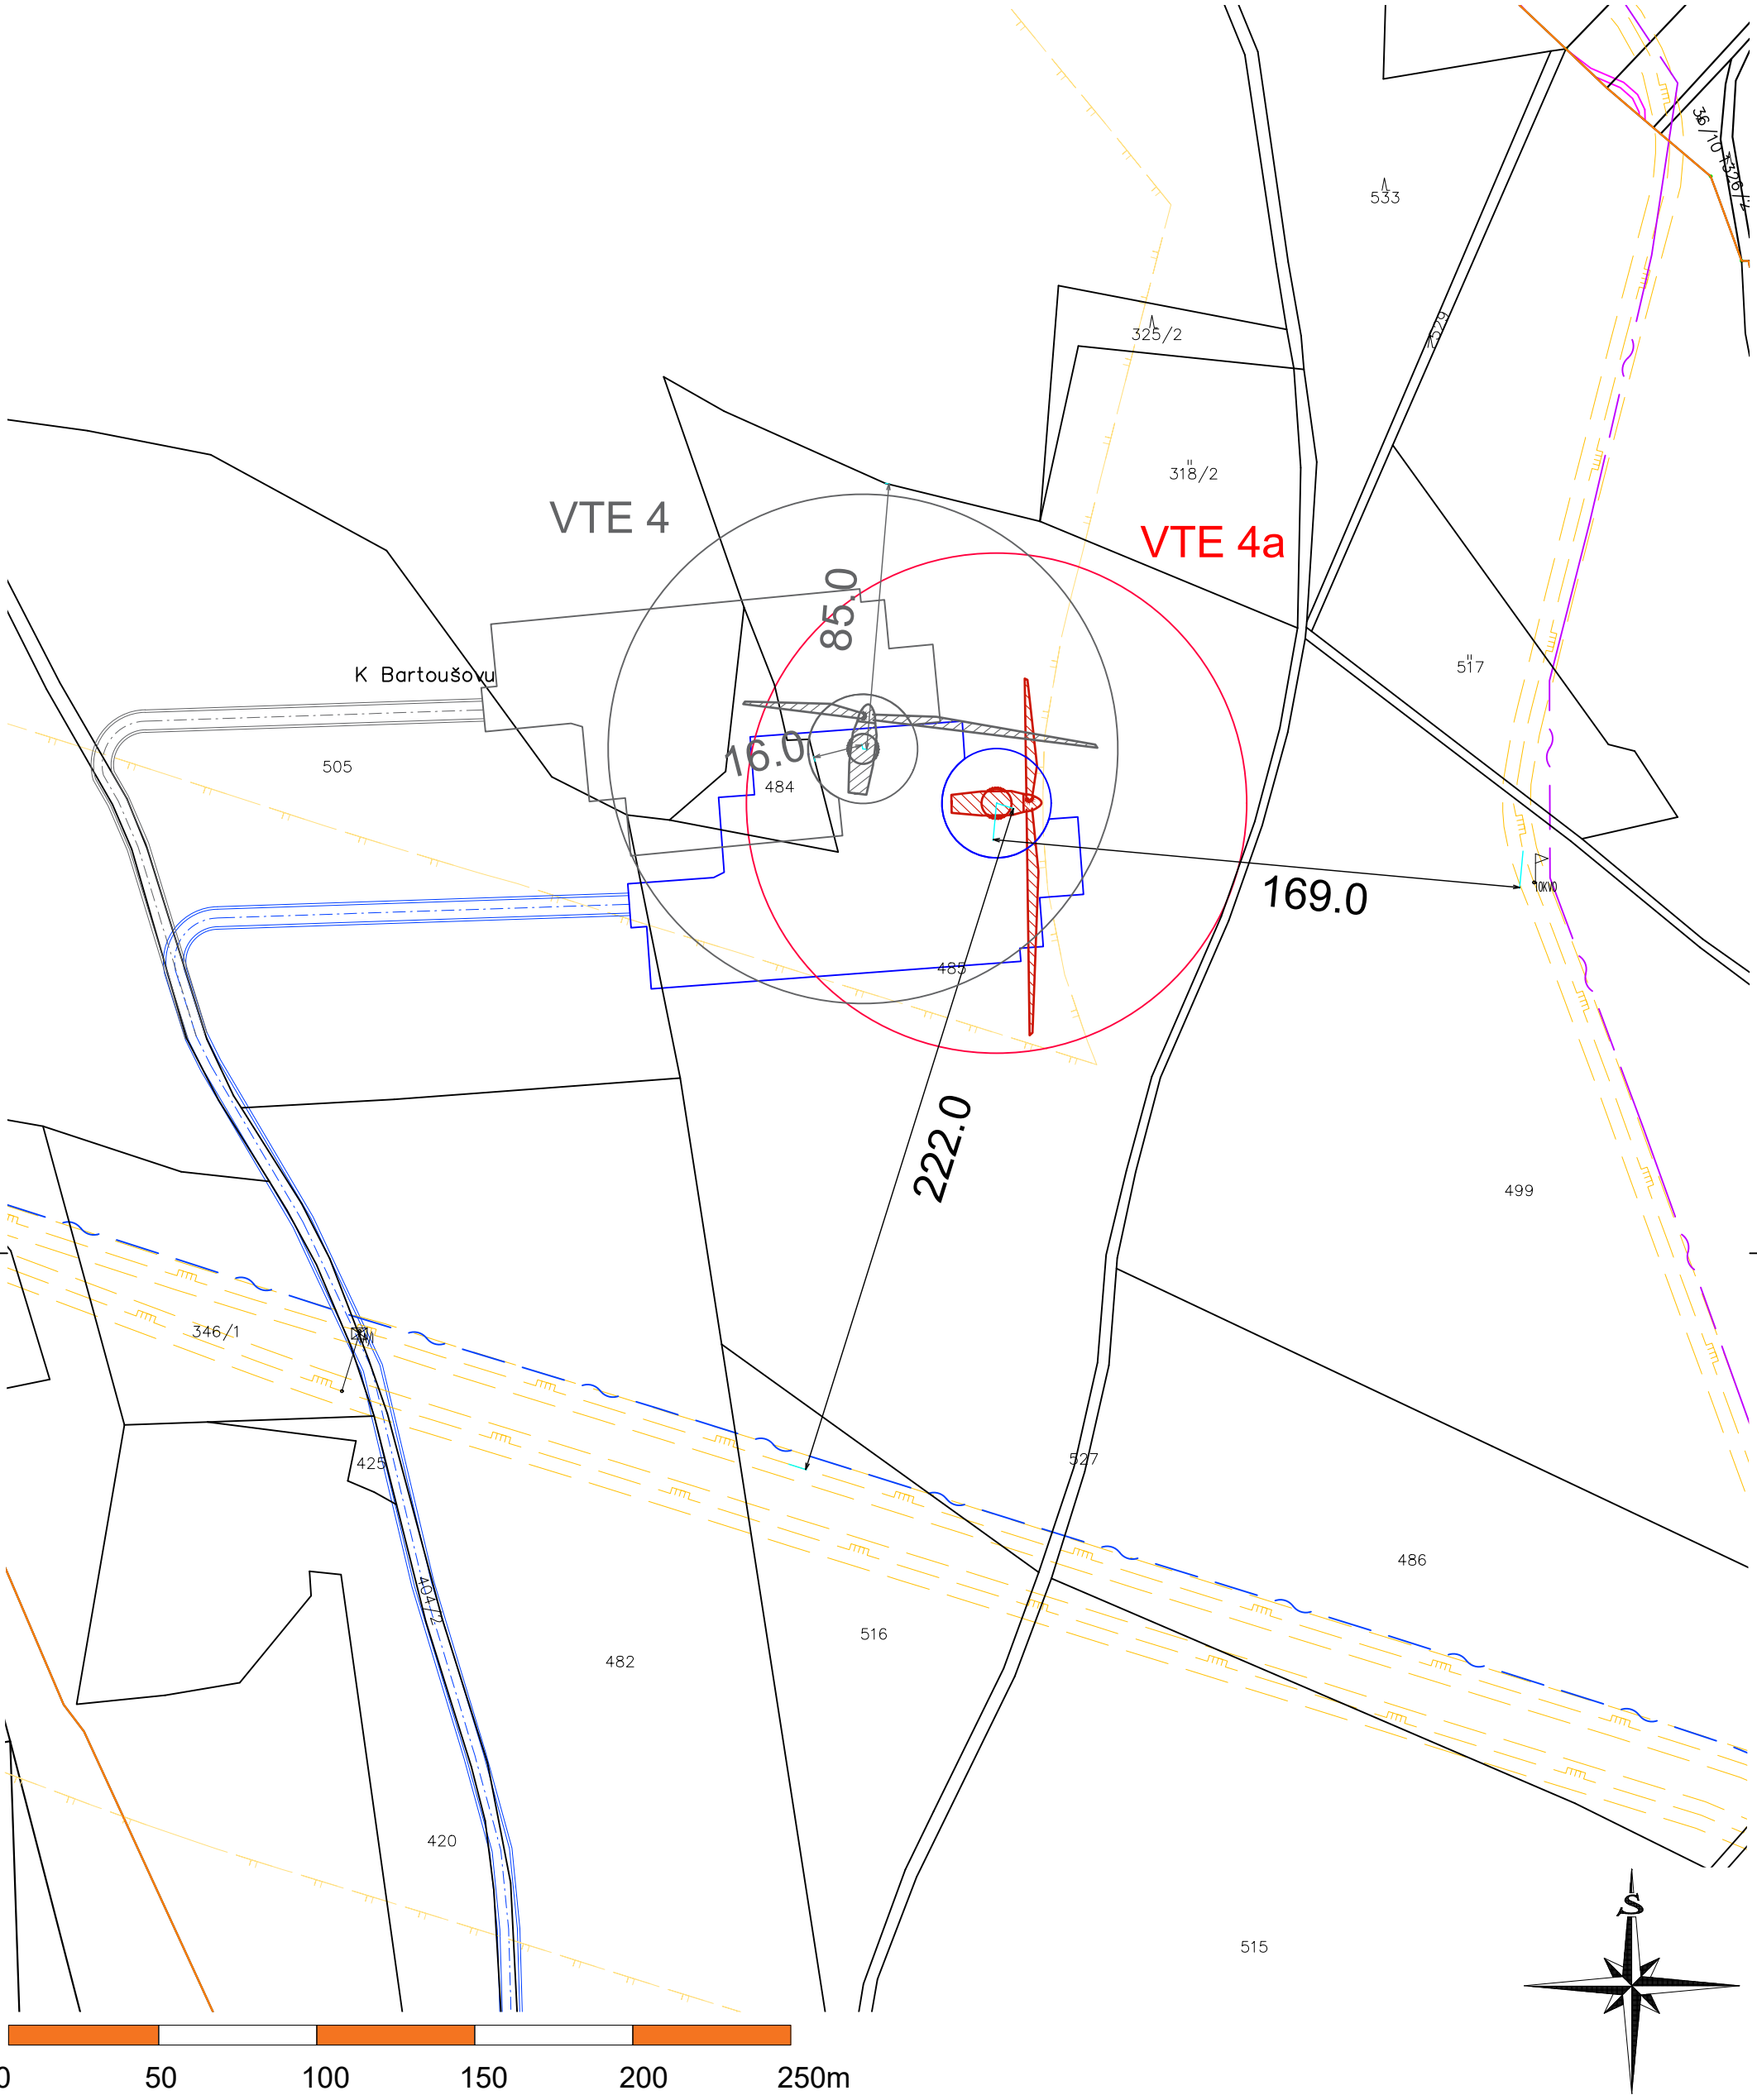

LEGENDA:

- Navržená větrná elektrárna
- Manipulační plocha a zařízení staveniště
- Přístupová komunikace
- Bezpečnostní pásmo plynovodu - VTL
- Ochranné pásmo VTL plynovodu
- Sdělovací vedení metalické
- Alternativní pozice VTE
- Sdělovací vedení optické
- Osa přístupové komunikace

Vypracoval:	Schválil:
Ing. David Havlíček	Jakub Hejna

ČEZ Obnovitelné zdroje, s.r.o.
Duhová 1444 / 2
Praha 4 - Michle 140 00

Investor: ČEZ, a. s.

Název stavby:

VTE Šlapanov

Objekt (SO), provozní celek (PC): VTE Šlapanov

Obsah výkresu:

Katastrální situační výkres

Datum:	03/2026
Stupeň dokumentace:	Studie
Měřítko:	1:2000
Formát:	A3
Revize:	
Číslo stavby:	-
Číslo výkresu:	Paré

04

VTE 5

VTE 1

85.0

15.0

2.0

11.0

121.0

111.0

73.0

0 50 100 150 200 250m

LEGENDA:


- Navržená větrná elektrárna
- Manipulační plocha a zařízení staveniště
- Přístupová komunikace
- Bezpečnostní pásmo plynovodu - VTL
- Ochranné pásmo VTL plynovodu
- Sdělovací vedení metalické
- VTL Plynovod - podzemní
- Sdělovací vedení optické
- Osa přístupové komunikace

Alternativní pozice VTE

Vypracoval: Ing. David Havlíček	Schválil: Jakub Hejna

ČEZ Obnovitelné zdroje, s.r.o.
Duhová 1444 / 2
Praha 4 - Michle 140 00

Investor:	ČEZ, a. s.
Název stavby:	**VTE Šlapanov**
Objekt (SO), provozní celek (PC):	VTE Šlapanov
Obsah výkresu:	**Katastrální situační výkres**
Datum:	03/2026
Stupeň dokumentace:	Studie
Měřítko:	1:2000
Formát:	A2
Revize:	
Číslo stavby:	-
Číslo výkresu:	**05**
	Paré

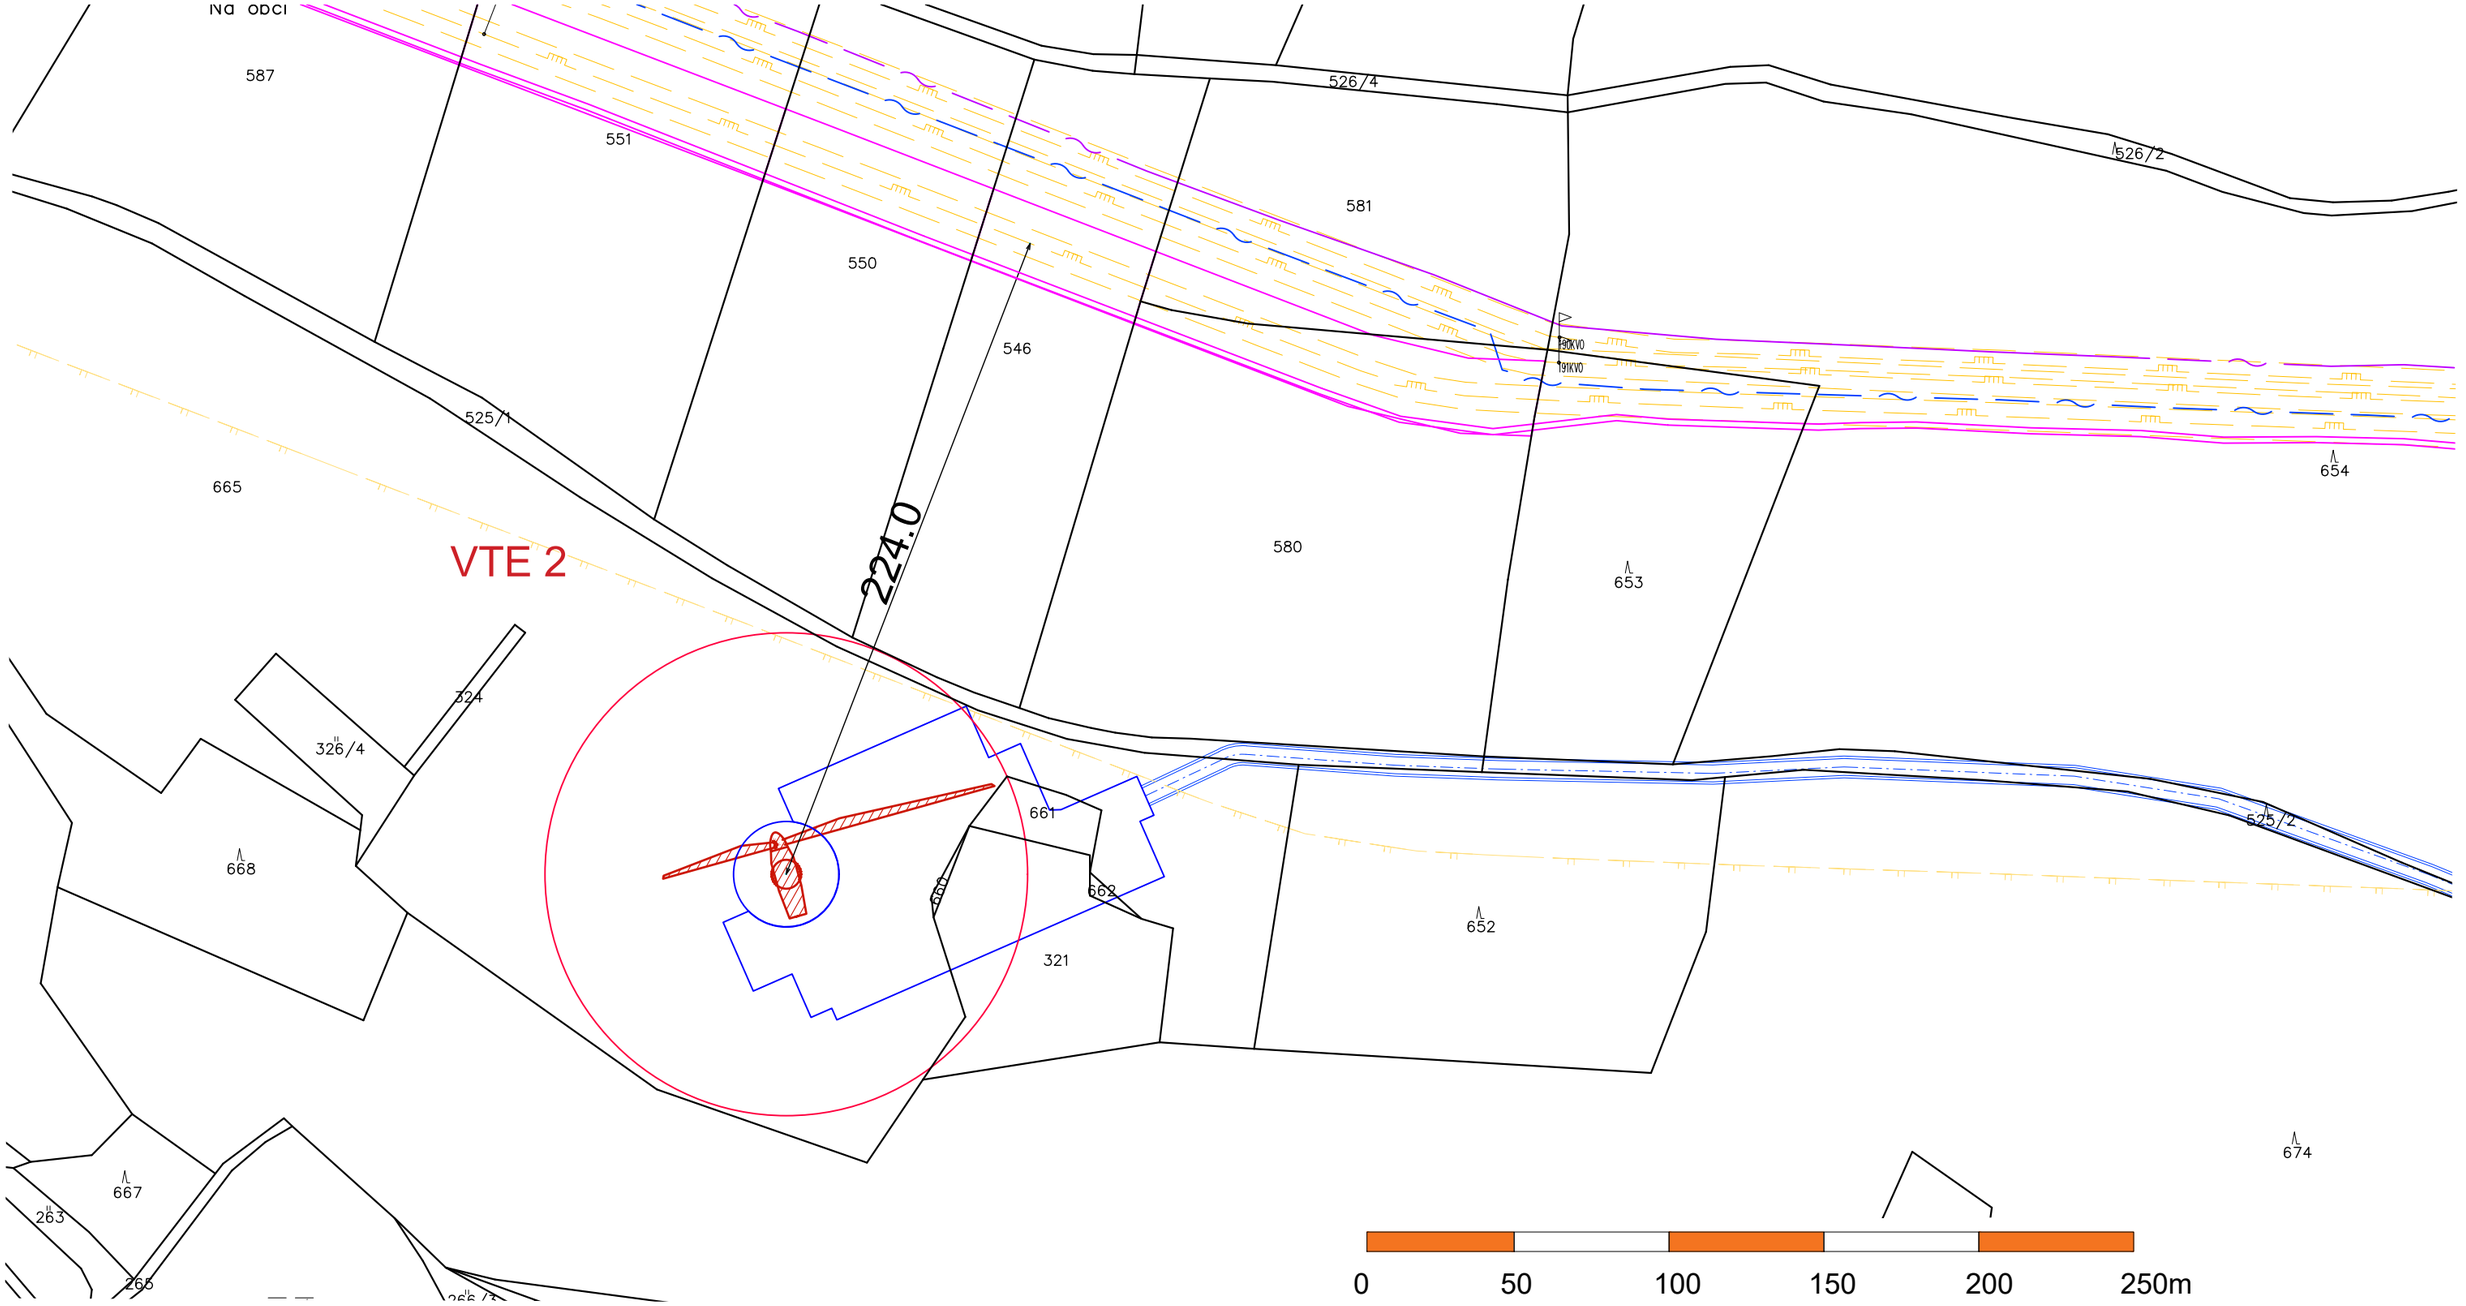

LEGENDA:

- Navržená větrná elektrárna
- Manipulační plocha a zařízení staveniště
- Přístupová komunikace
- Bezpečnostní pásmo plynovodu - VTL
- Ochranné pásmo VTL plynovodu
- Sdělovací vedení metalické
- VTL Plynovod - podzemní
- Sdělovací vedení optické
- Osa přístupové komunikace

Vypracoval: Ing. David Havlíček	Schválil: Jakub Hejna
ČEZ Obnovitelné zdroje, s.r.o. Duhová 1444 / 2 Praha 4 - Michle 140 00	
Investor: ČEZ, a. s.	Datum: 03/2026
	Stupeň dokumentace: Studie
Název stavby: **VTE Šlapanov**	Měřítko: 1:2000
	Formát: A3
	Revize:
	Číslo stavby: -
Objekt (SO), provozní celek (PC): VTE Šlapanov	Číslo výkresu: **06** Paré
Obsah výkresu: **Katastrální situační výkres**	